



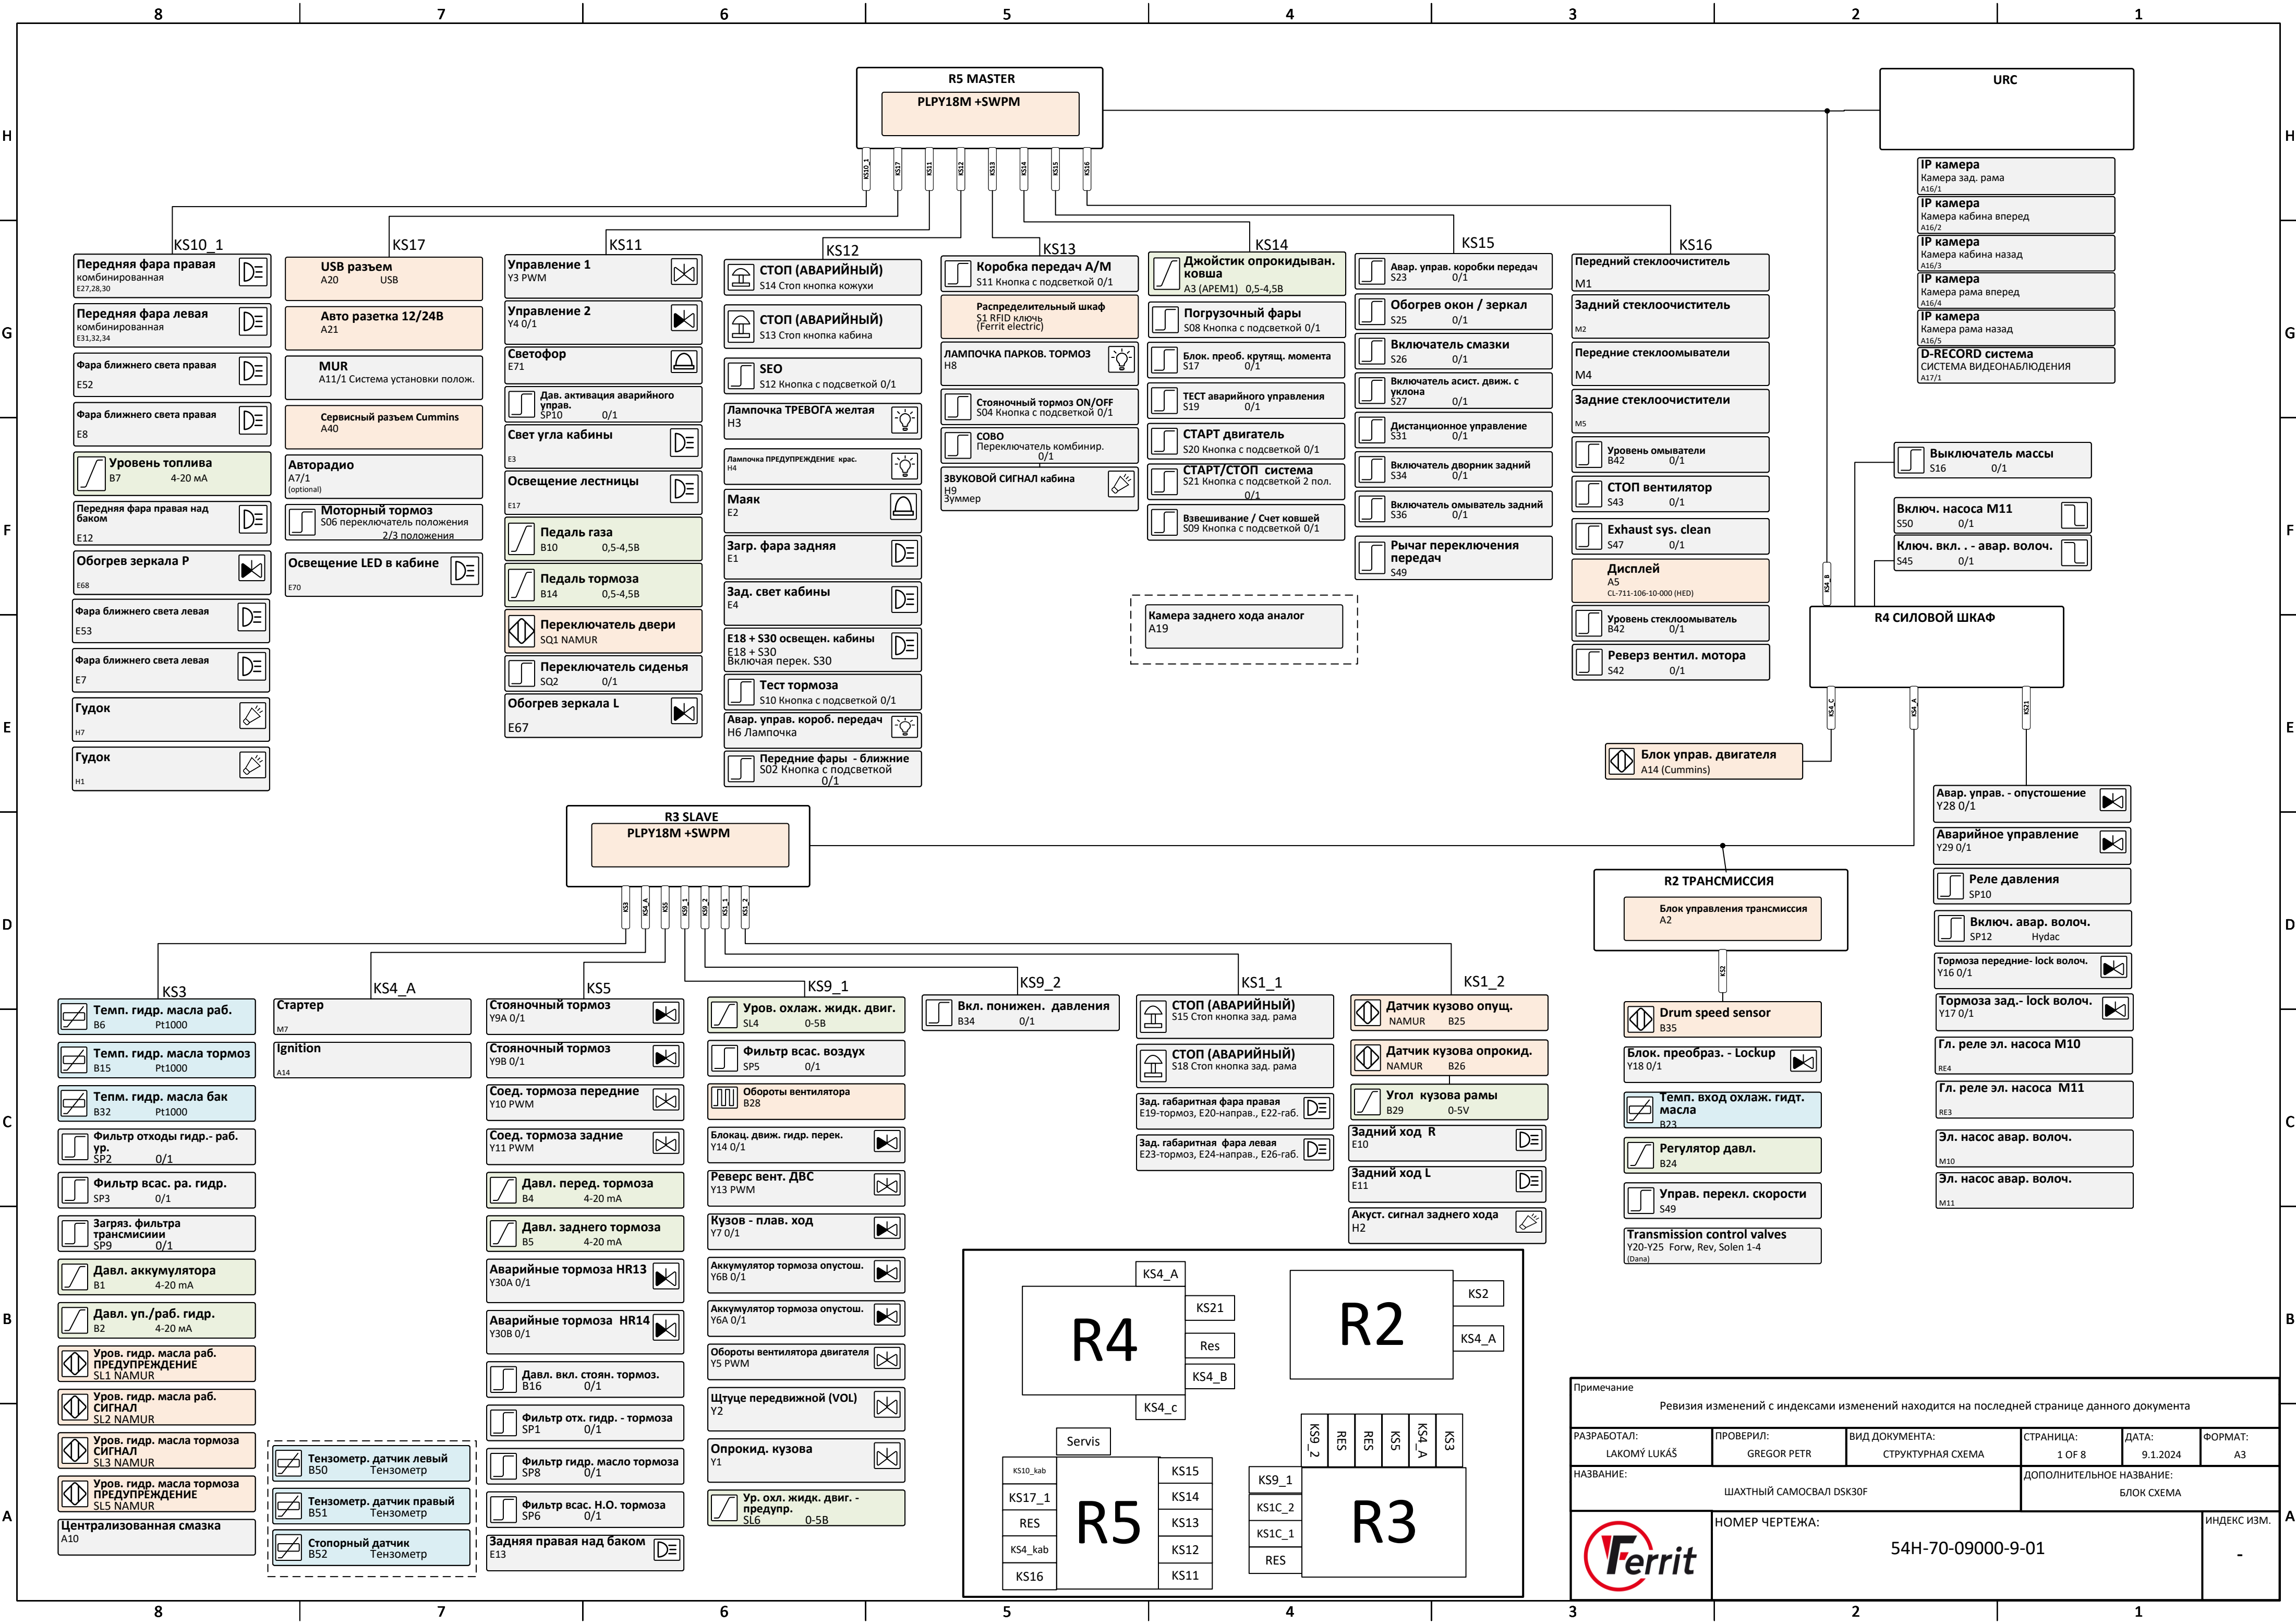

Примечание Ревизия изменений с индексами изменений находится на последней странице данного документа					
РАЗРАБОТАЛ: LAKOMÝ LUKÁŠ	ПРОВЕРИЛ: GREGOR PETR	ВИД ДОКУМЕНТА: СТРУКТУРНАЯ СХЕМА	СТРАНИЦА: 1 OF 8	ДАТА: 9.1.2024	ФОРМАТ: A3
НАЗВАНИЕ: ШАХТНЫЙ САМОСВАЛ DSK30F			ДОПОЛНИТЕЛЬНОЕ НАЗВАНИЕ: БЛОК СХЕМА		
НОМЕР ЧЕРТЕЖА: 		54H-70-09000-9-01			ИНДЕКС ИЗМ. -

R2 - KS2 - Deutsch 31p				
HDP26-24-31PE-L017				
Pin	Раз.	Сигнал	Сечен. провод.[мм2]	
1	Y18	U+ Блок_преобр.	1,5	
2	Y18	GND_преобр.	1,5	
3	Y20	U+ FORWARD	1,5	
4	Y20	GND_Y20	1,5	
5	Y21	U+ REVERSE	1,5	
6	Y21	GND_Y21	1,5	
7	Y22	U+ SOLENOID_1	1,5	
8	Y22	GND_Y22	1,5	
9	Y23	U+ SOLENOID_2	1,5	
10	Y23	GND_Y23	1,5	
11	Y24	U+ SOLENOID_3	1,5	
12	Y24	GND_Y24	1,5	
13	Y25	U+ SOLENOID_4_Neutra	1,5	
14	Y25	GND_Y25	1,5	
15	B35	U+ выход_1	1	
16	B35	GND_B35	1	
17	B24	GND_A	1	
18	B24	5V_B	1	
19	B24	Pressure_C	1	
20	B23	темпер_охлаж_1	1	
21	B23	GND_B23	1	
22		резерв1	1	
23		резерв2	1	
24				
25				
26				
27				
28				
29				
30				
31				

R2 Блок управления коробки передач		
HDP26-18-14PE-L01 ??		
Pin	Раз.	Сигнал
A	R2	U+ R2_a
B	R2	U+ R2_b
C	R2	GND_R2
D	R2	CAN_H
E	R2	CAN_L
F	R2	СПИДОМЕТР_IMP
G	R2	КОРОБ.ПЕРЕДАЧ_АВАР. РЕЖИМ
H	R2	АВАРИЙН_РЕЖИМ_FORWARD
J	R2	АВАРИЙН_РЕЖИМ_REVERSE
K	R2	FWD_S49
L	R2	REV_S49
M	R2	UP_S49
N	R2	DOWN_S49
P	R2	ignition_R2

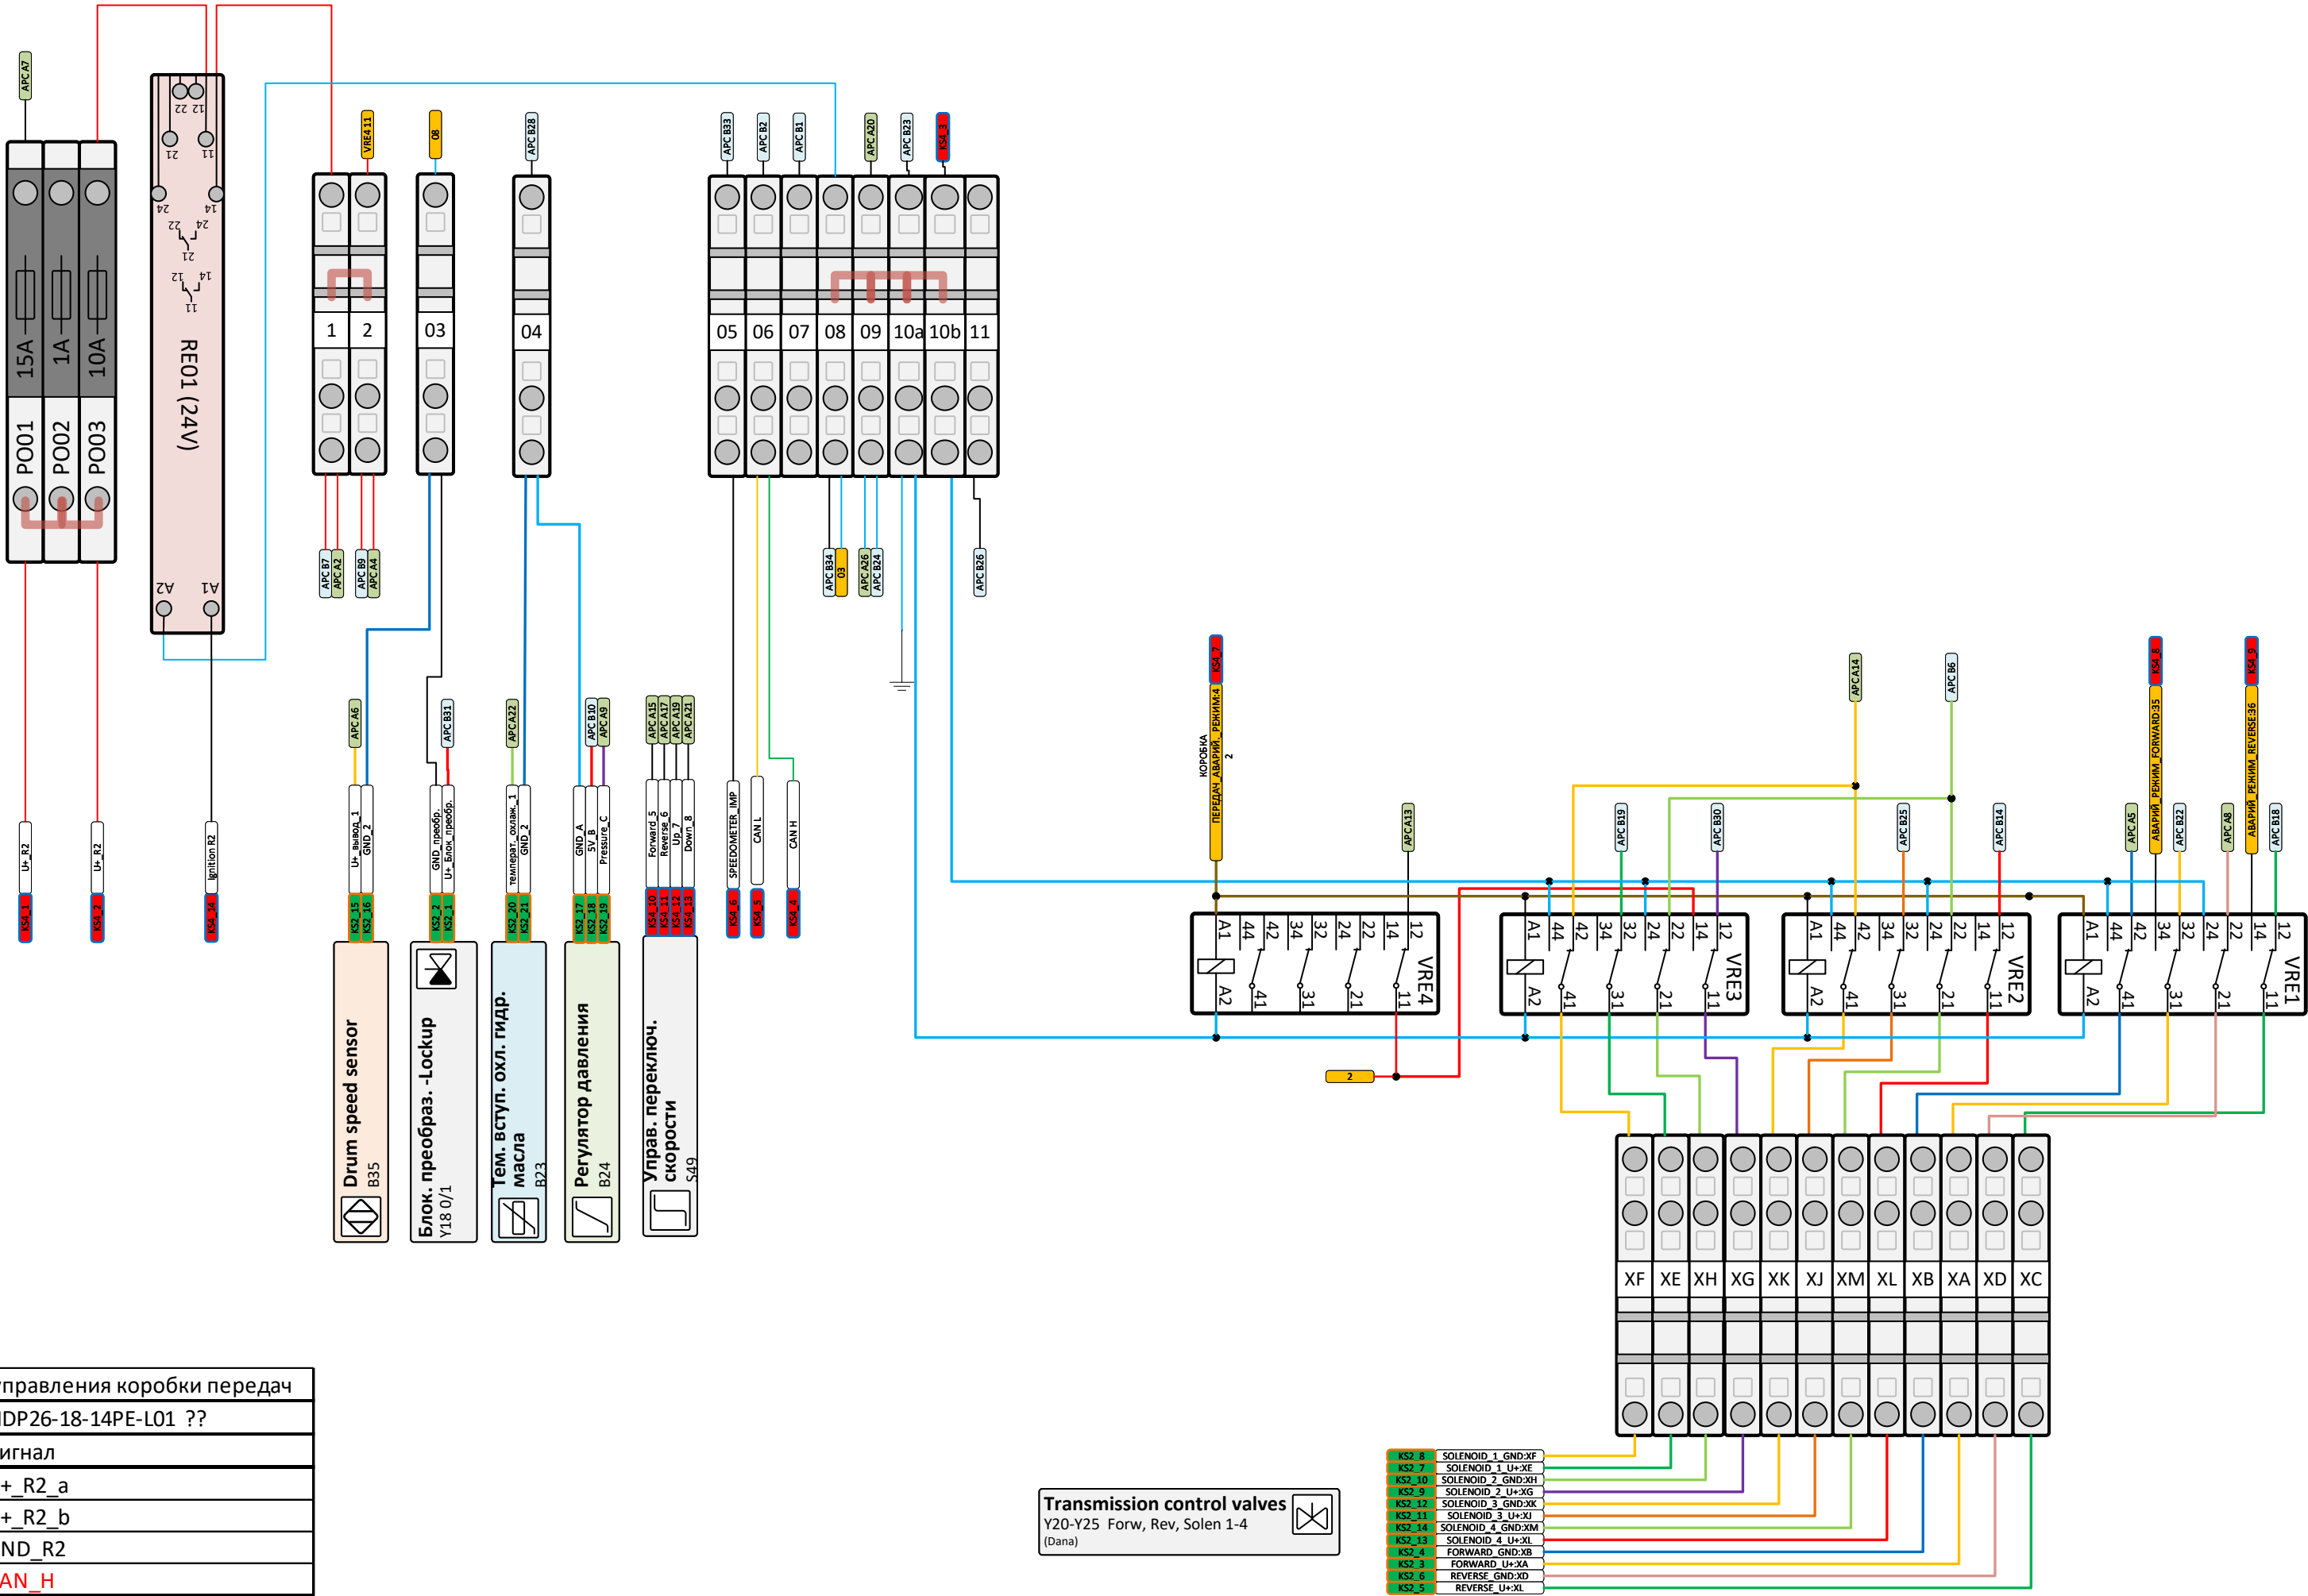


X20	SOLENOID_1_GND_XF
X21	SOLENOID_1_U+_XF
X22	SOLENOID_2_GND_XH
X23	SOLENOID_2_U+_XH
X24	SOLENOID_3_GND_XK
X25	SOLENOID_3_U+_XK
X26	SOLENOID_4_GND_XM
X27	SOLENOID_4_U+_XM
X28	FORWARD_GND_XB
X29	FORWARD_U+_XA
X30	REVERSE_GND_XD
X31	REVERSE_U+_XL

Transmission control valves
Y20-Y25 Forw, Rev, Solen 1-4
(Dana)







Примечание: Ревизия изменений с индексами изменений находится на последней странице данного документа.				
РАЗРАБОТАЛ: ЛАКОМЪ LUKAŠ	ПРОВЕРИЛ: GREGOR PETR	ВИД ДОКУМЕНТА: СТРУКТУРНАЯ СХЕМА	СТРАНИЦА: 2 OF 8	ДАТА: 9.1.2024
НАЗВАНИЕ: ШАХТНЫЙ САМОСВАЛ DSK30F			ДОПОЛНИТЕЛЬНОЕ НАЗВАНИЕ: РАСПРЕДЕЛИТЕЛЬ R2 КОРОБКА ПЕРЕДАЧ	
НОМЕР ЧЕРТЕЖА: 54H-70-09000-9-01				ИНДЕКС ИЗМ.: E

Плата РLPY18М (Р)

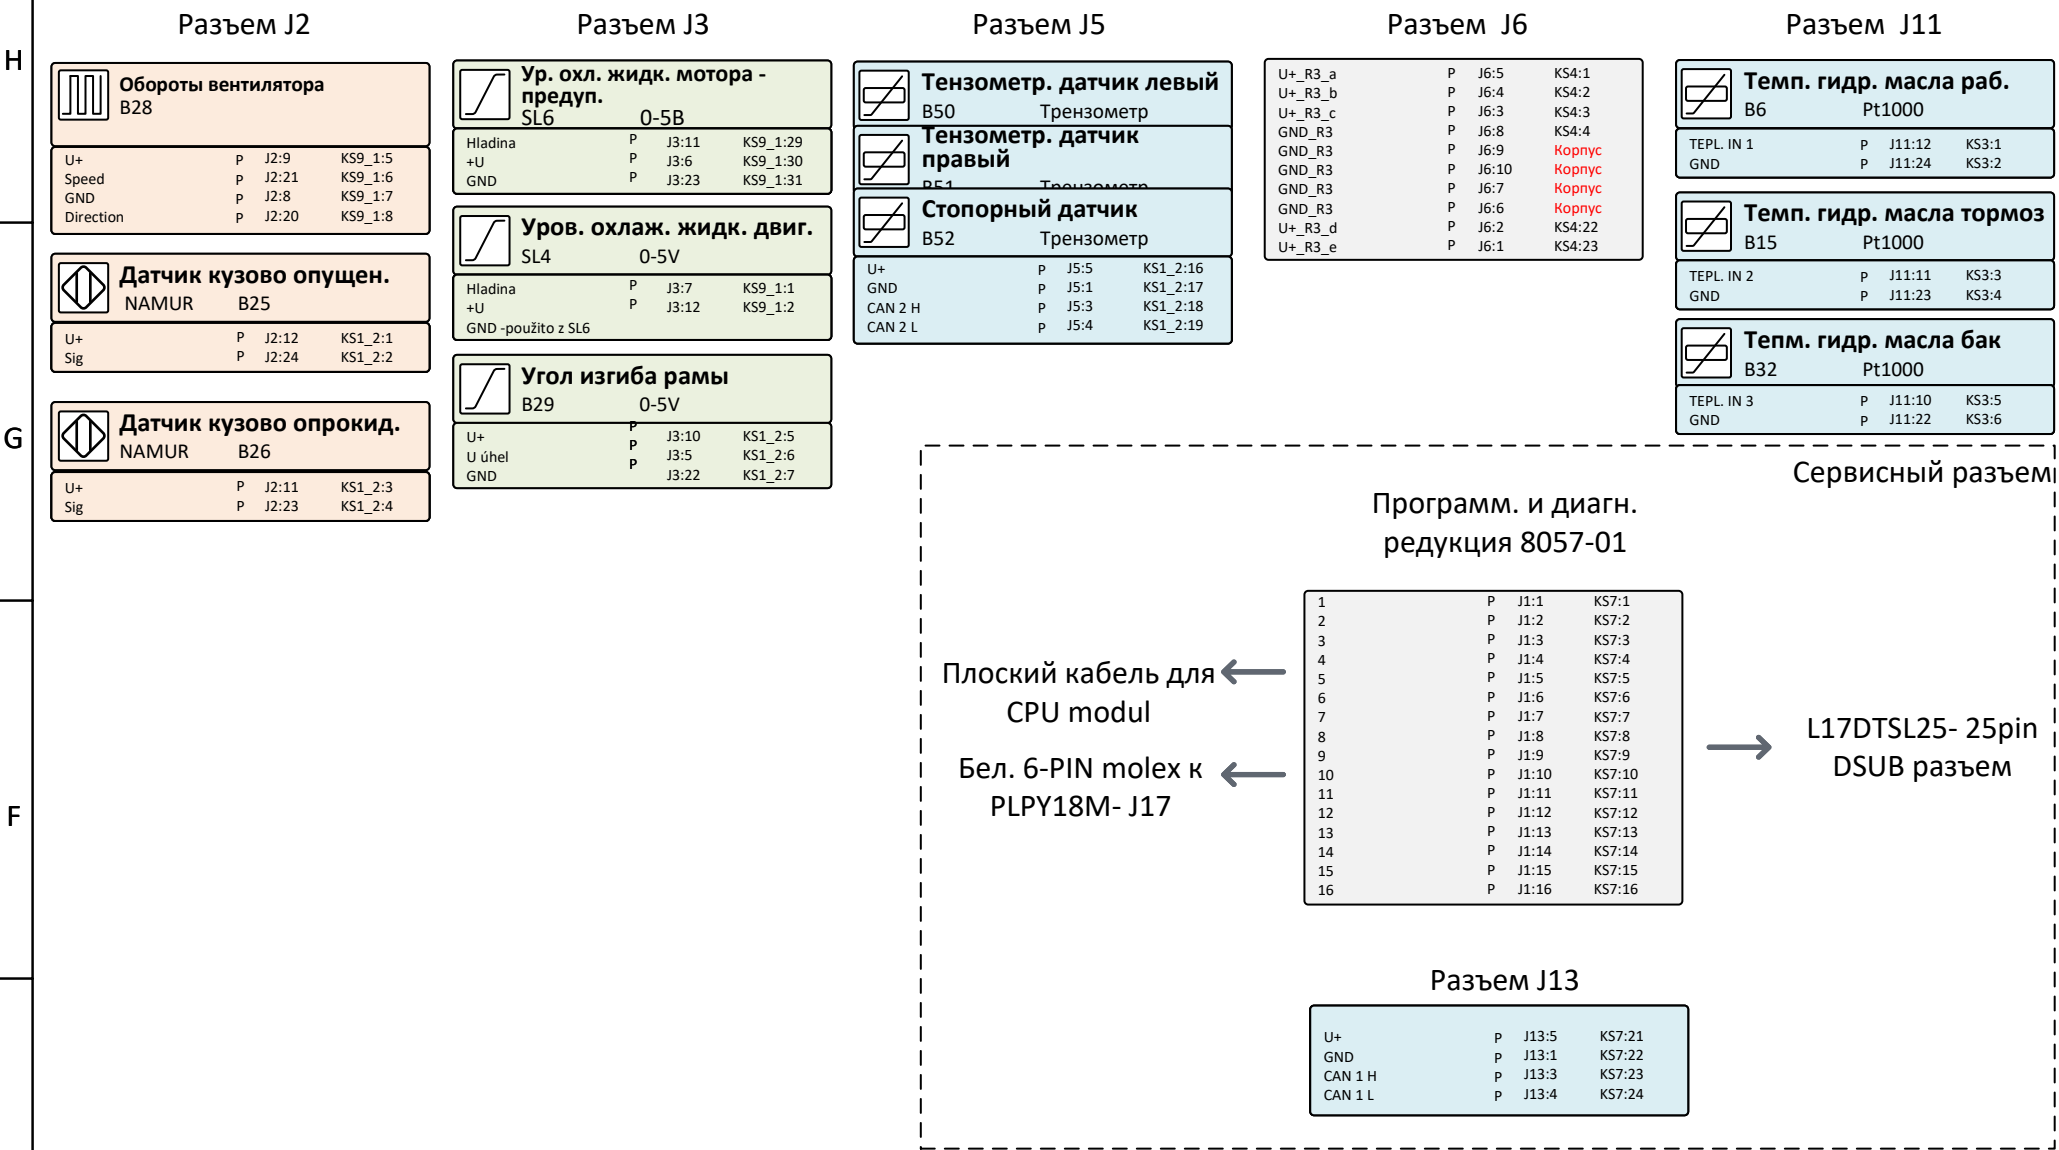

Плата SW панель (S)

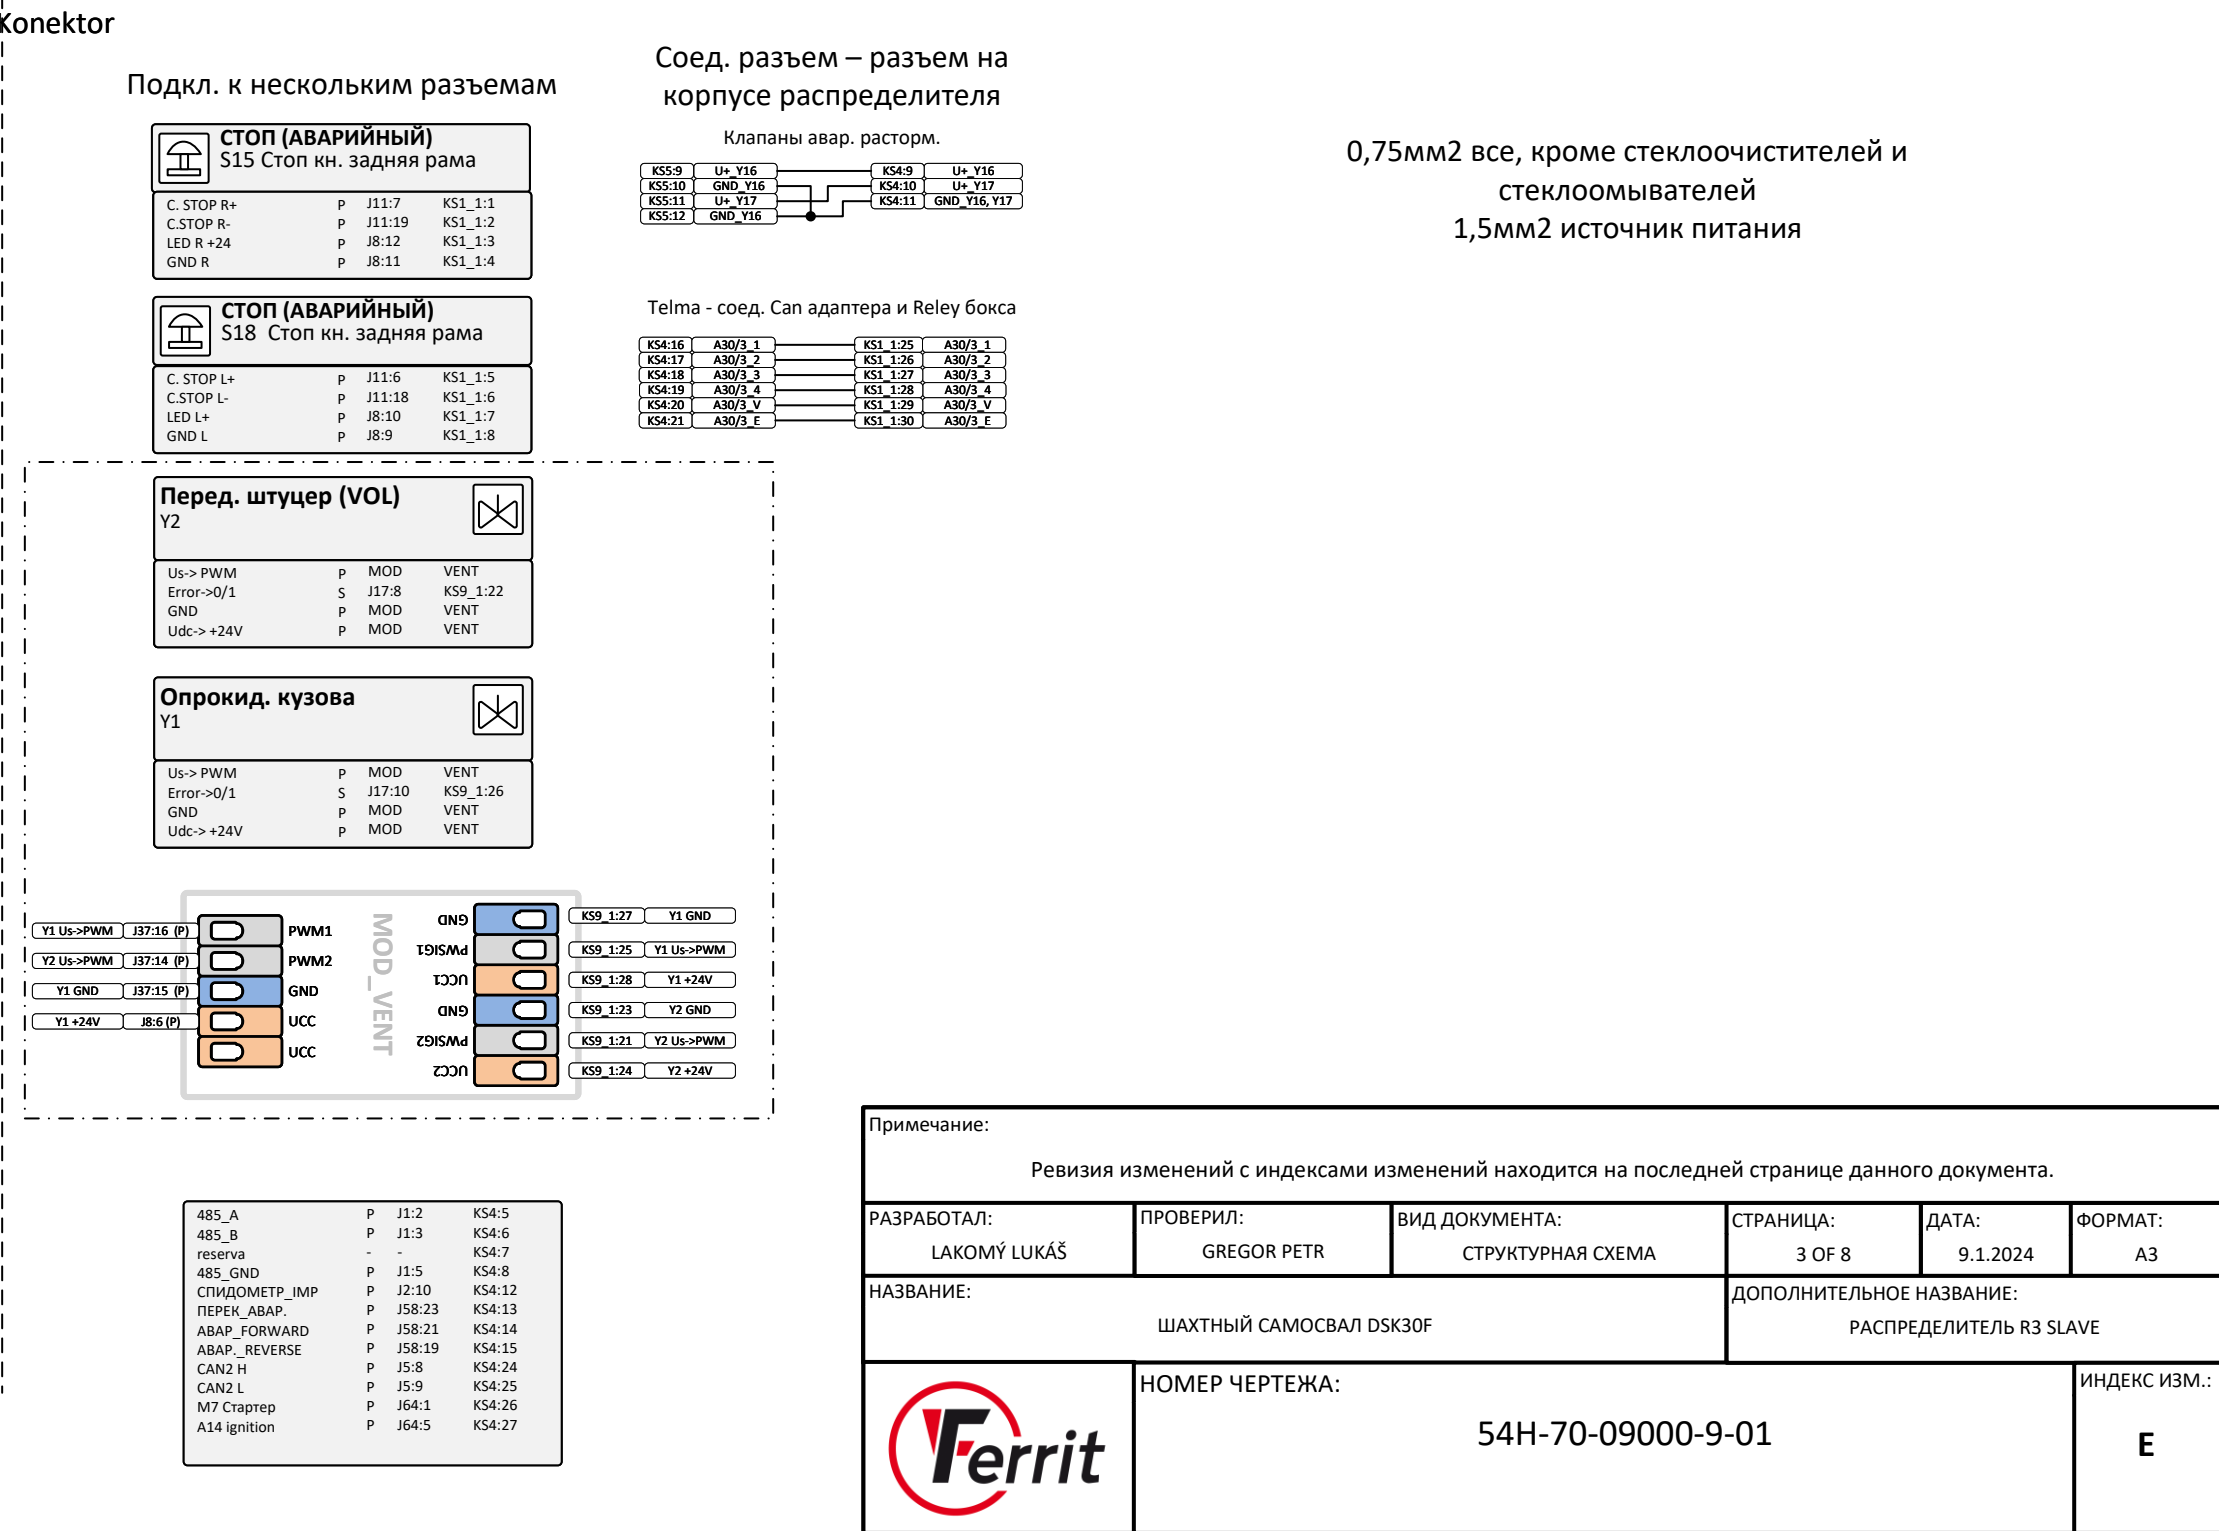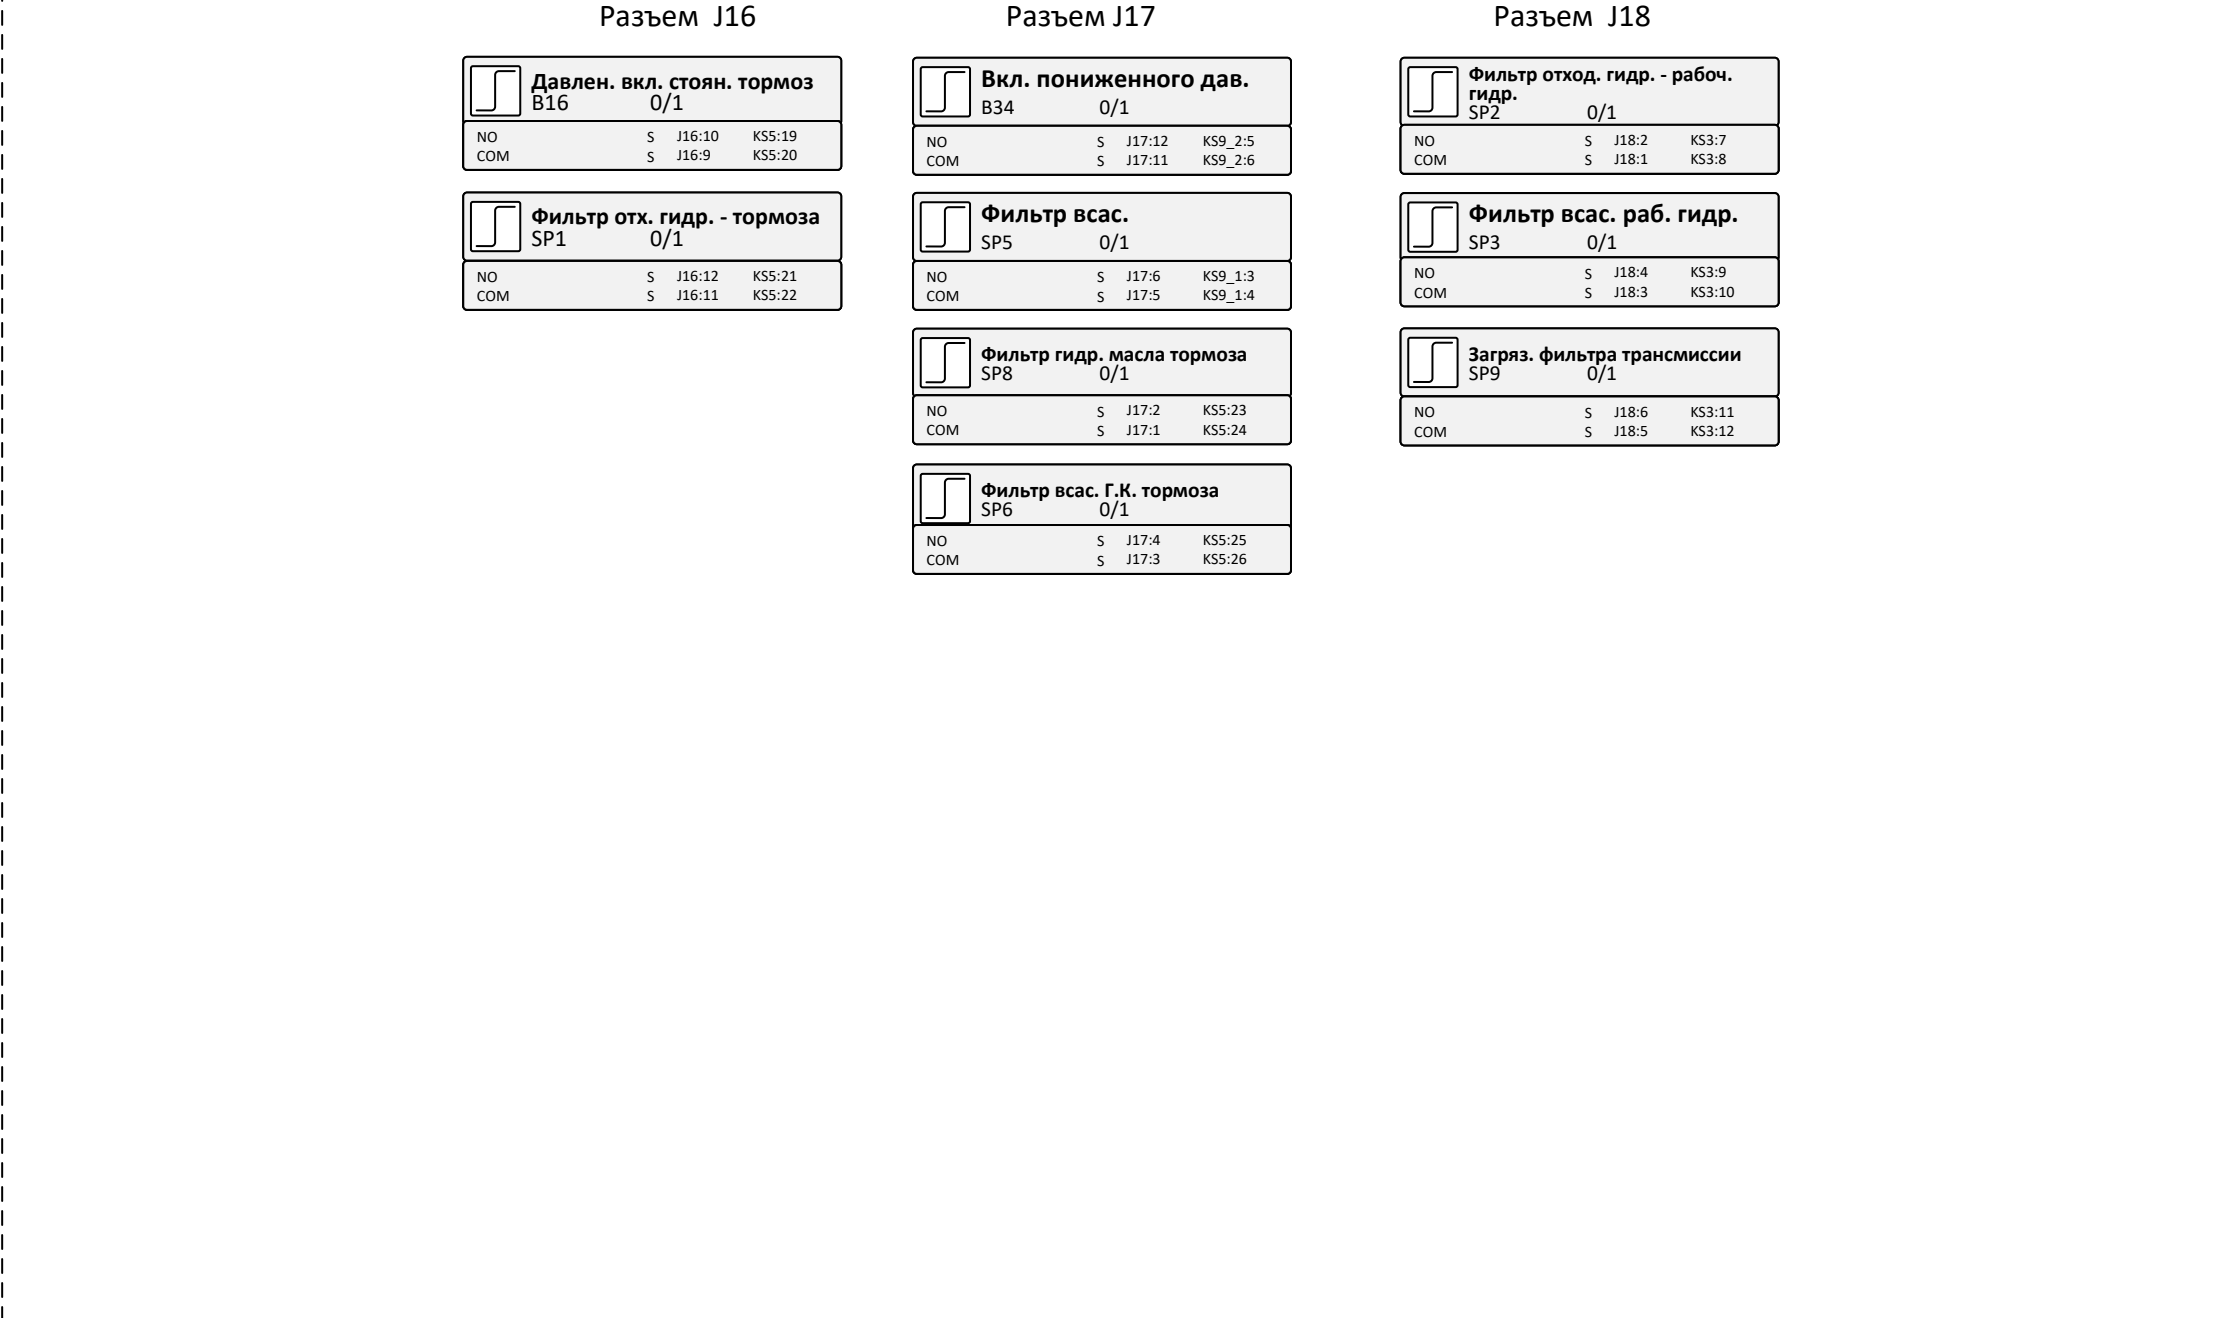


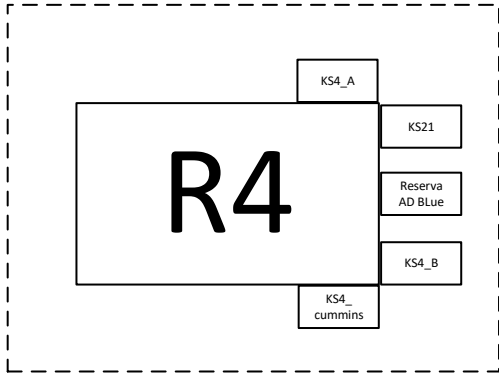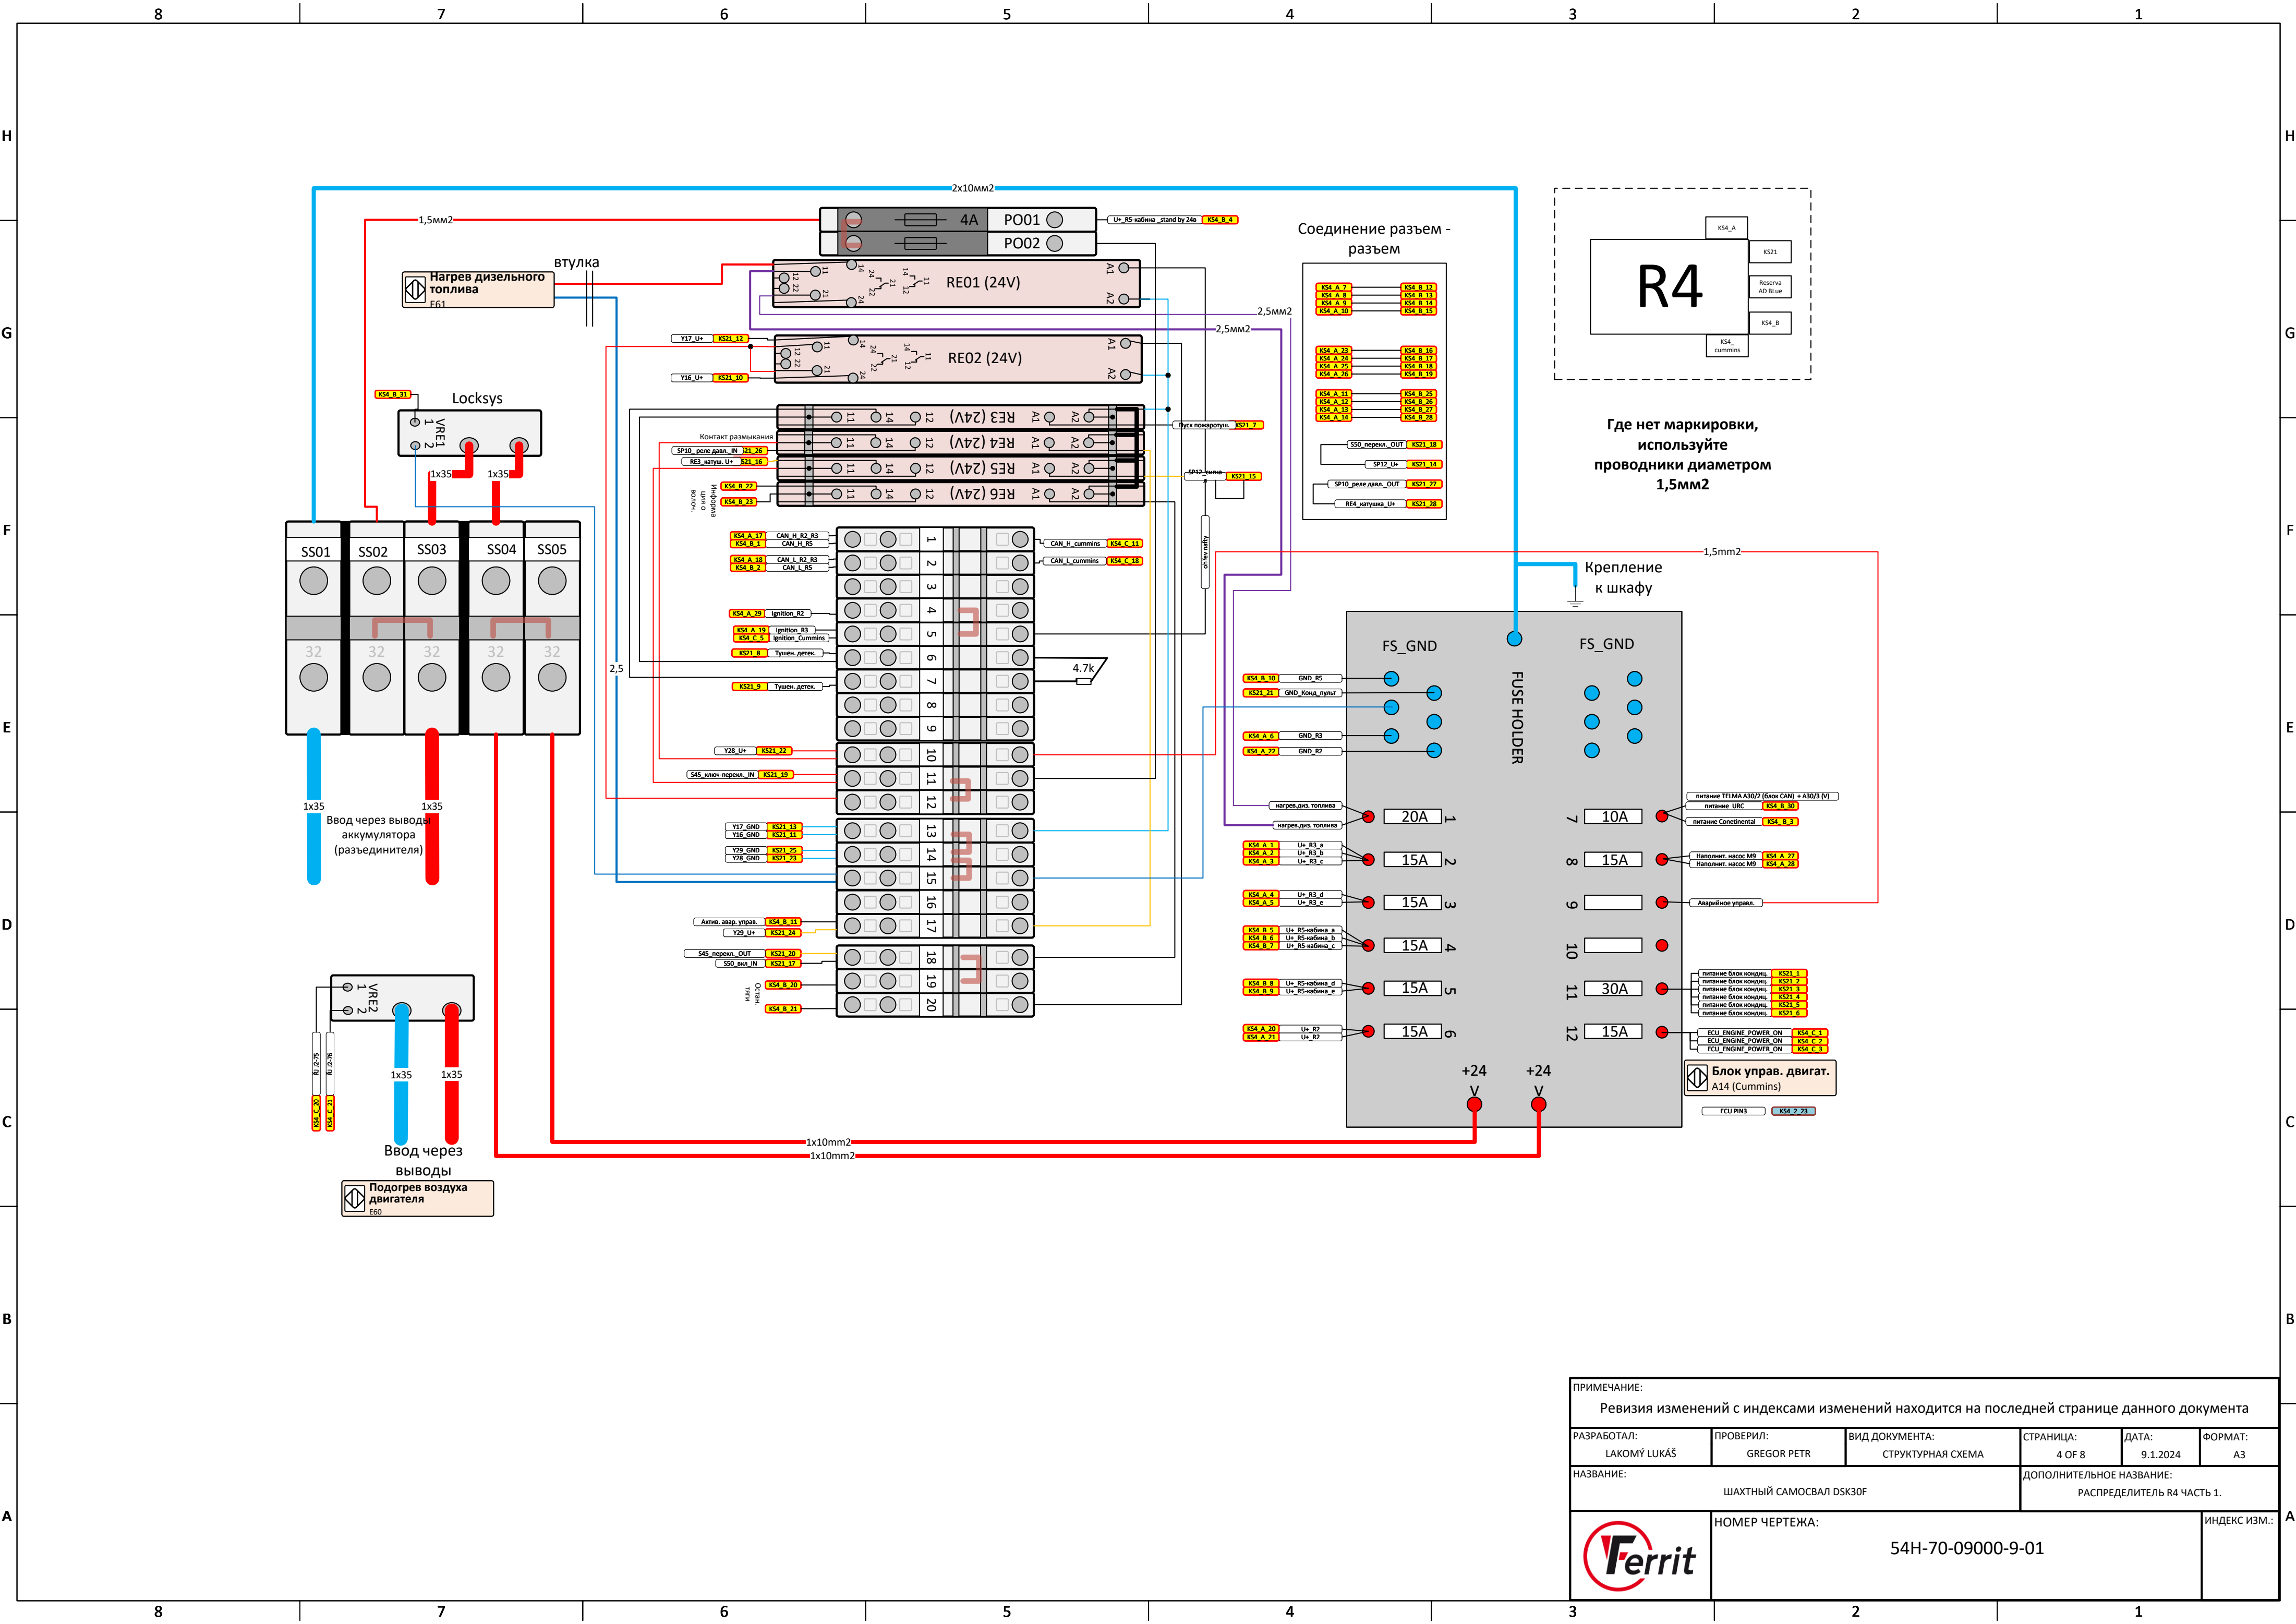

Где нет маркировки,
используйте
проводники диаметром
1,5мм2







Крепление
к шкафу

ПРИМЕЧАНИЕ: Ревизия изменений с индексами изменений находится на последней странице данного документа					
РАЗРАБОТАЛ: LAKOMÝ LUKÁŠ	ПРОВЕРИЛ: GREGOR PETR	ВИД ДОКУМЕНТА: СТРУКТУРНАЯ СХЕМА	СТРАНИЦА: 4 OF 8	ДАТА: 9.1.2024	ФОРМАТ: A3
НАЗВАНИЕ: ШАХТНЫЙ САМОСВАЛ DSK30F			ДОПОЛНИТЕЛЬНОЕ НАЗВАНИЕ: РАСПРЕДЕЛИТЕЛЬ R4 ЧАСТЬ 1.		
		НОМЕР ЧЕРТЕЖА: 54Н-70-09000-9-01			ИНДЕКС ИЗМ.:

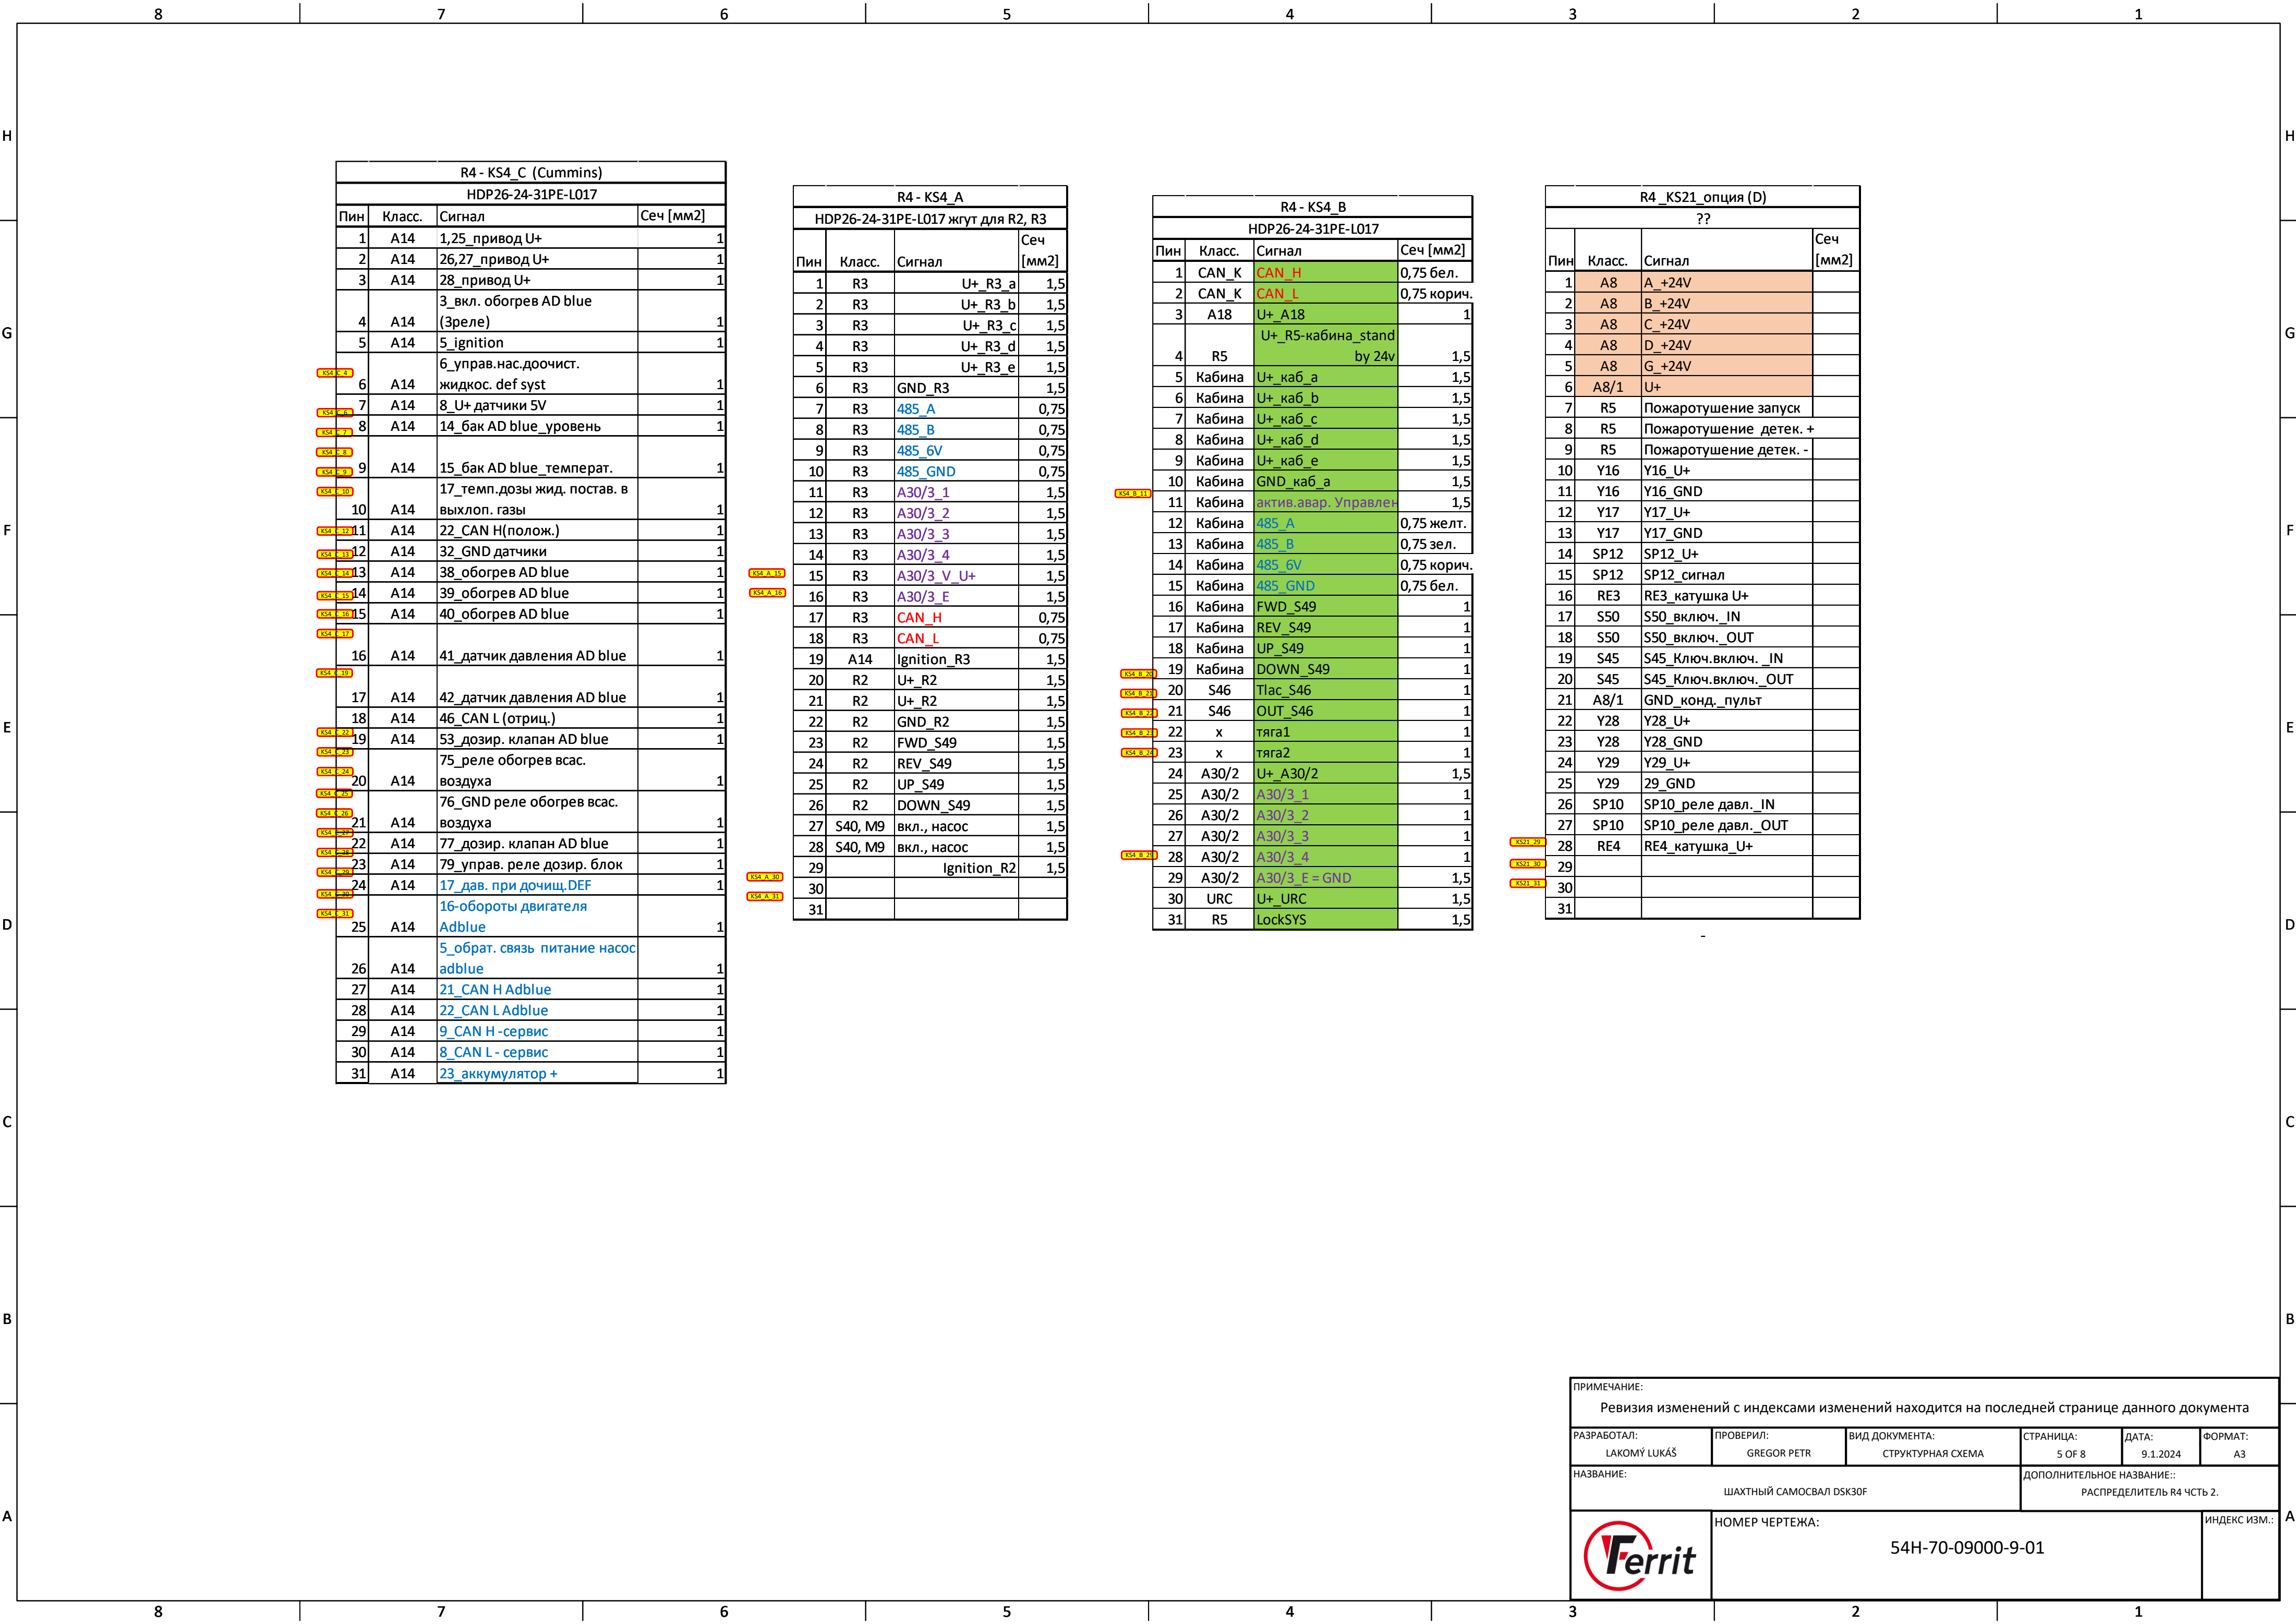

Плата PLPY18M (P)

Плата SW panel (S)

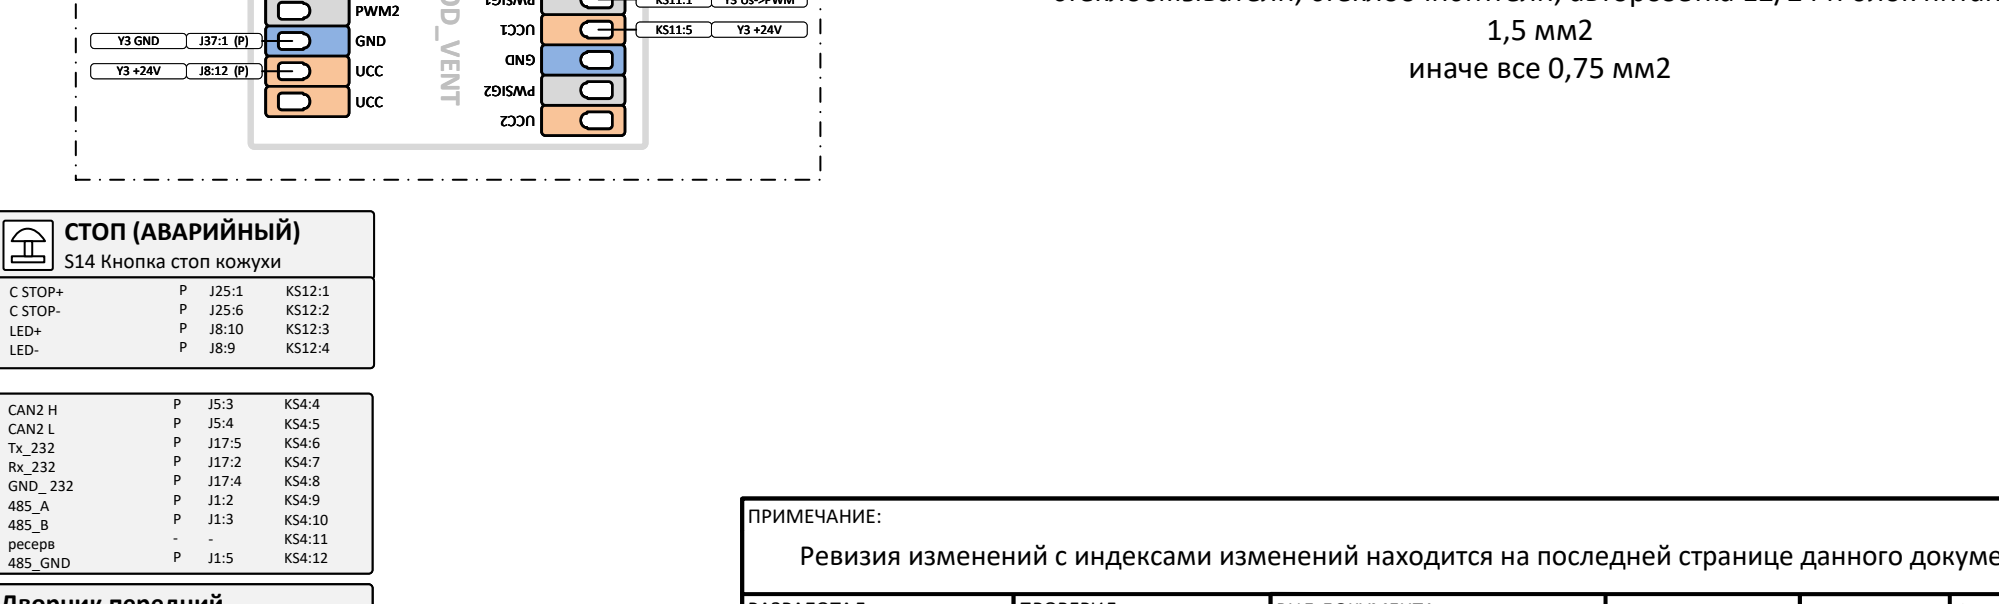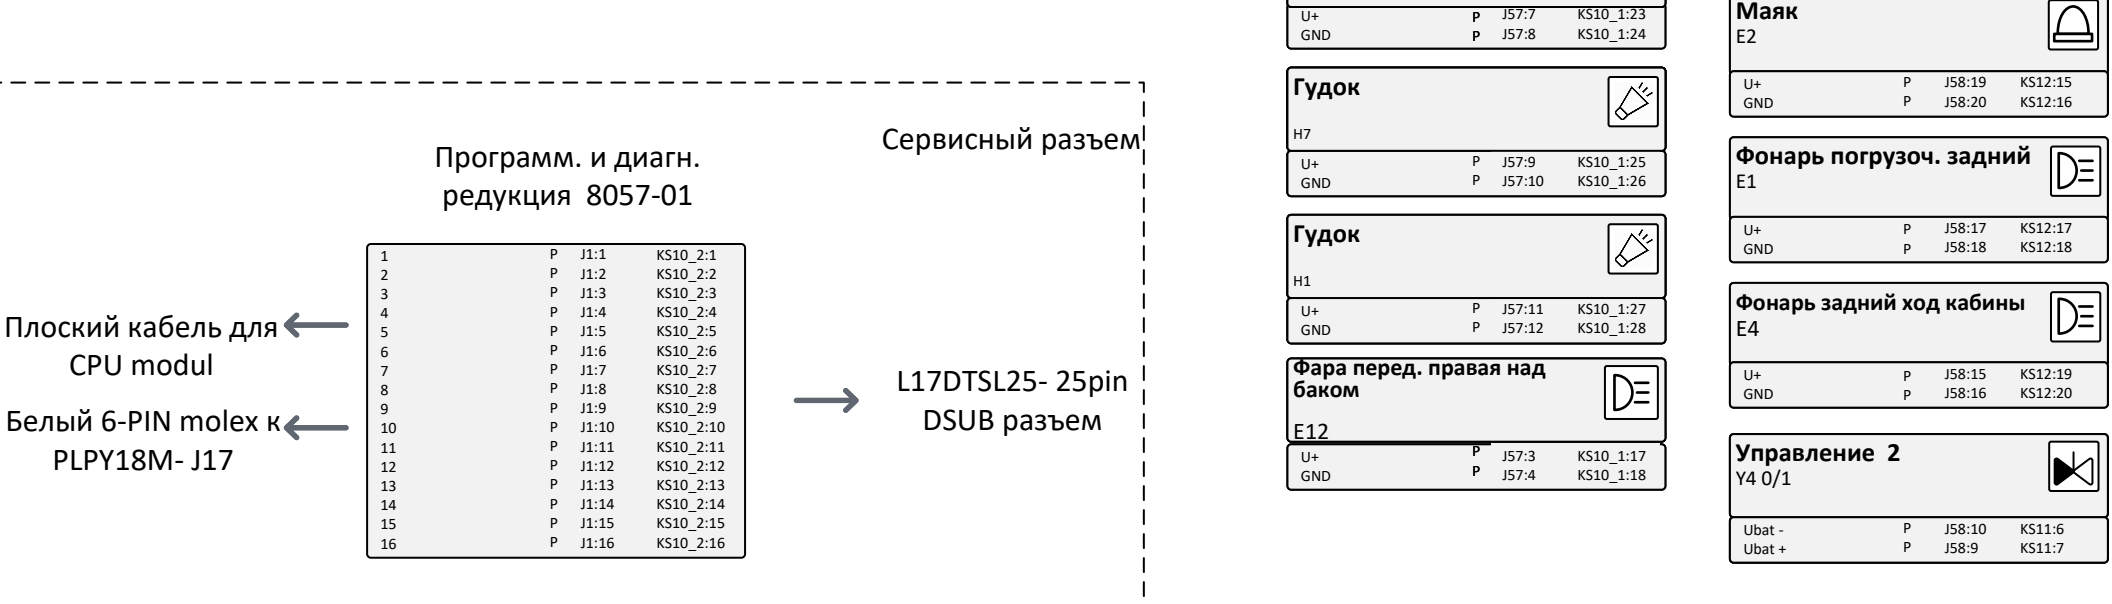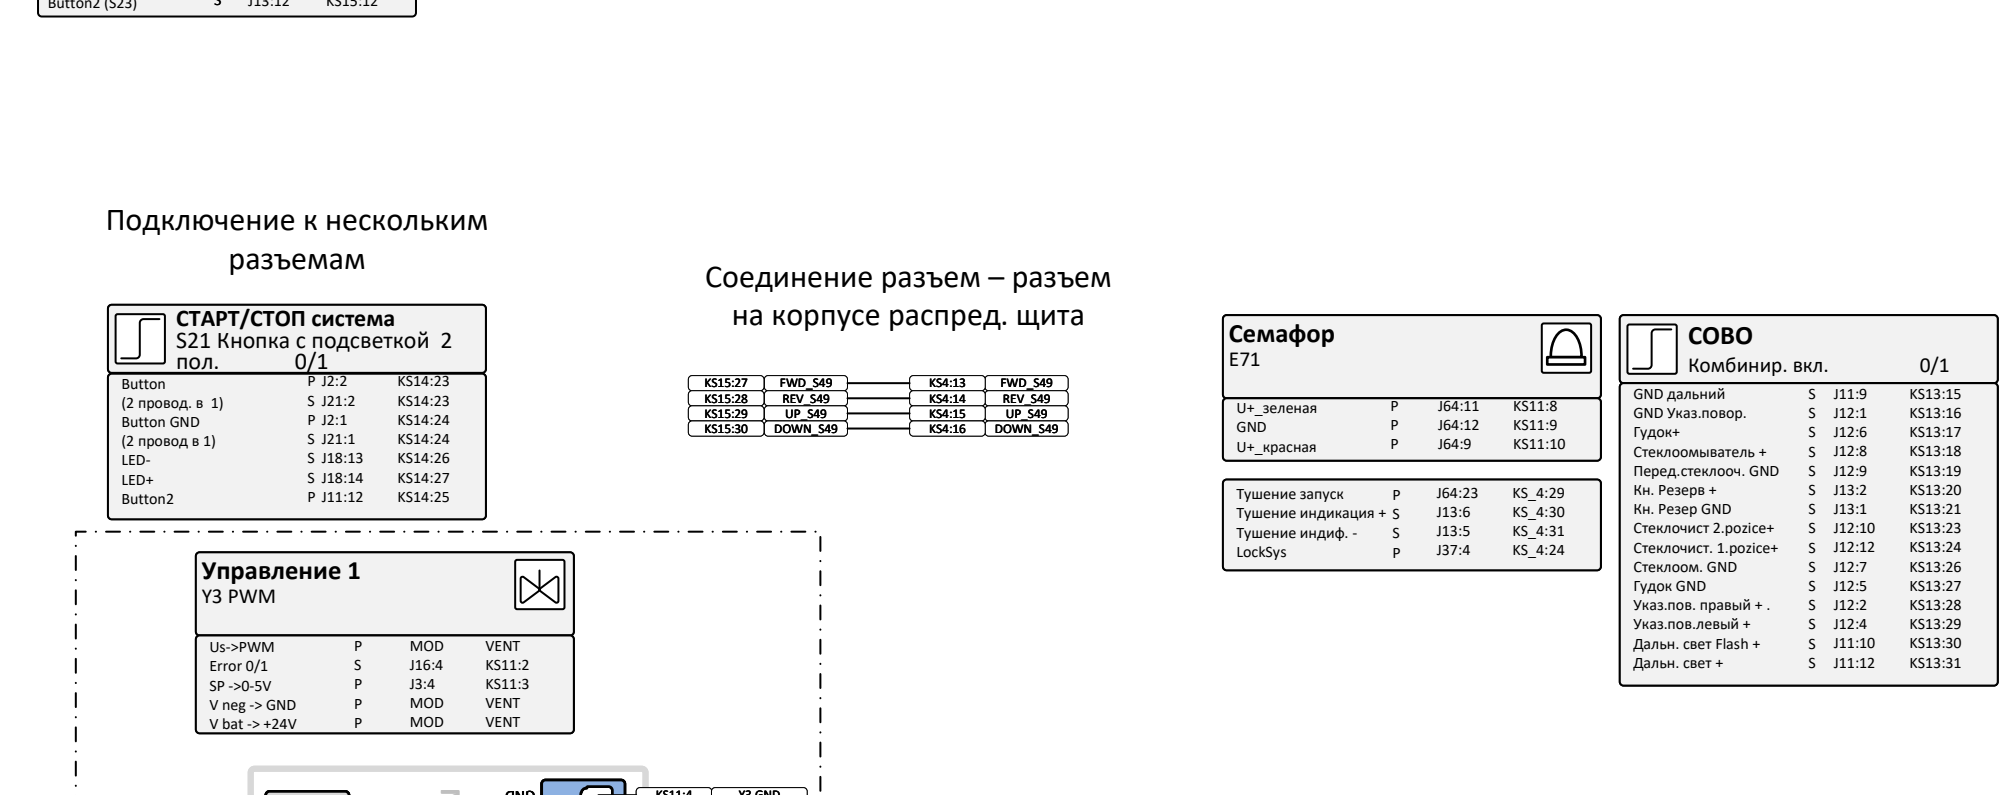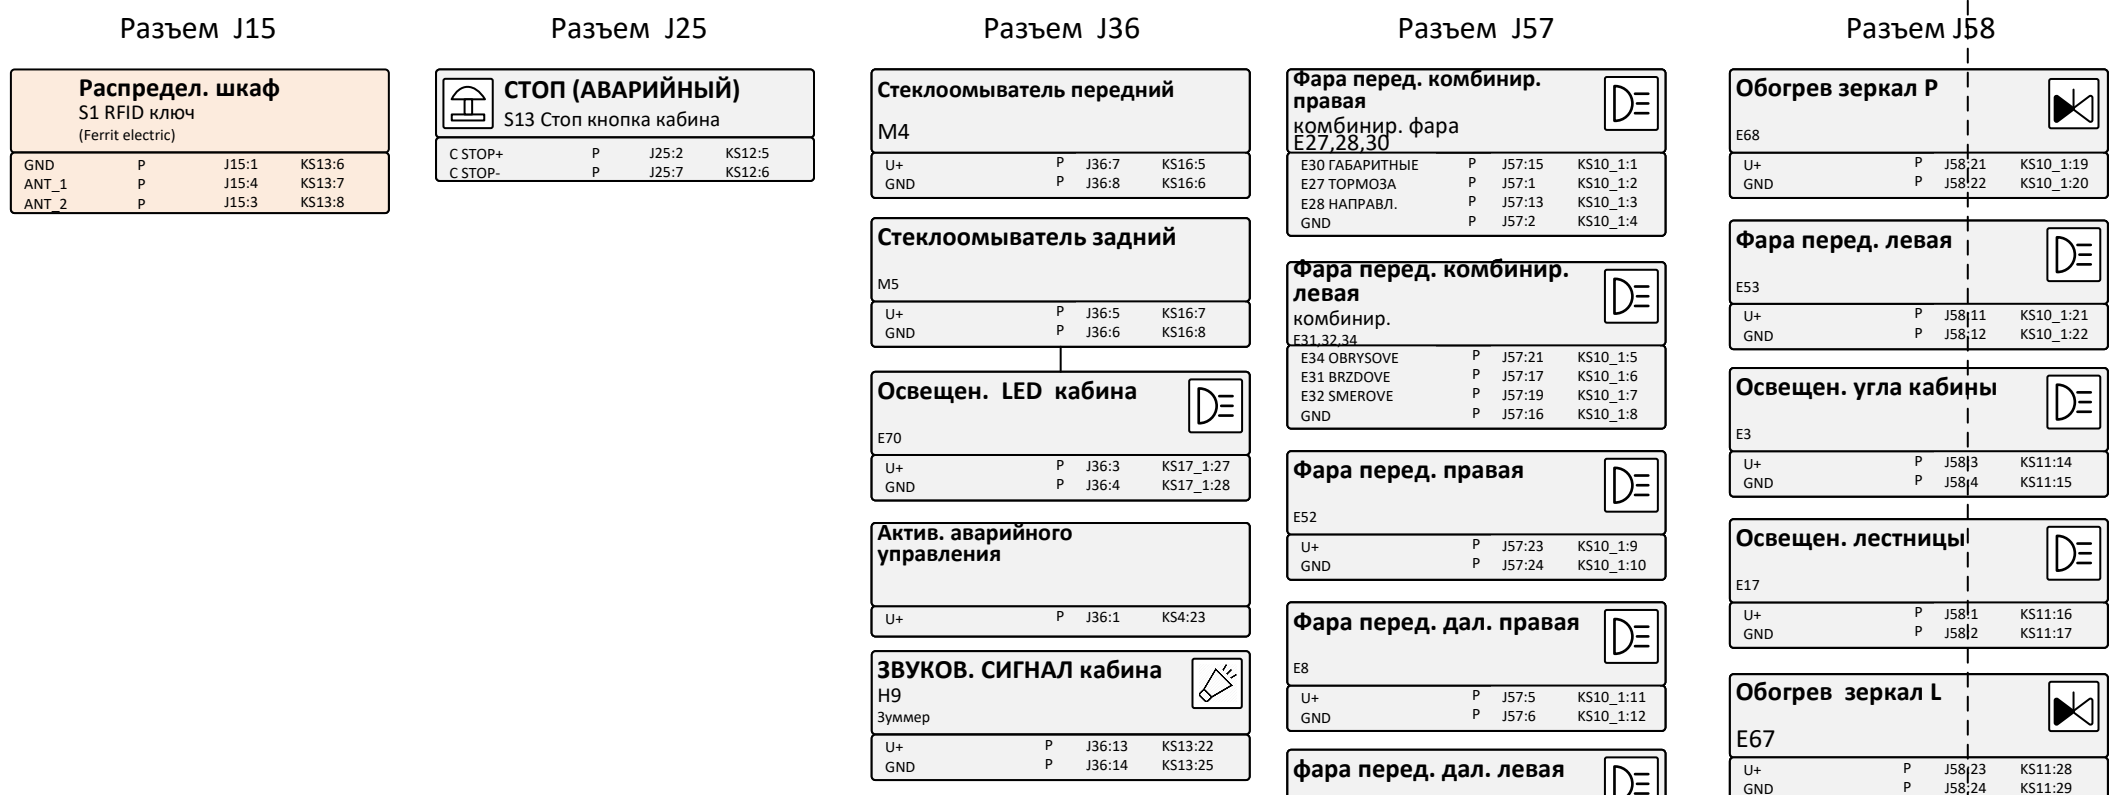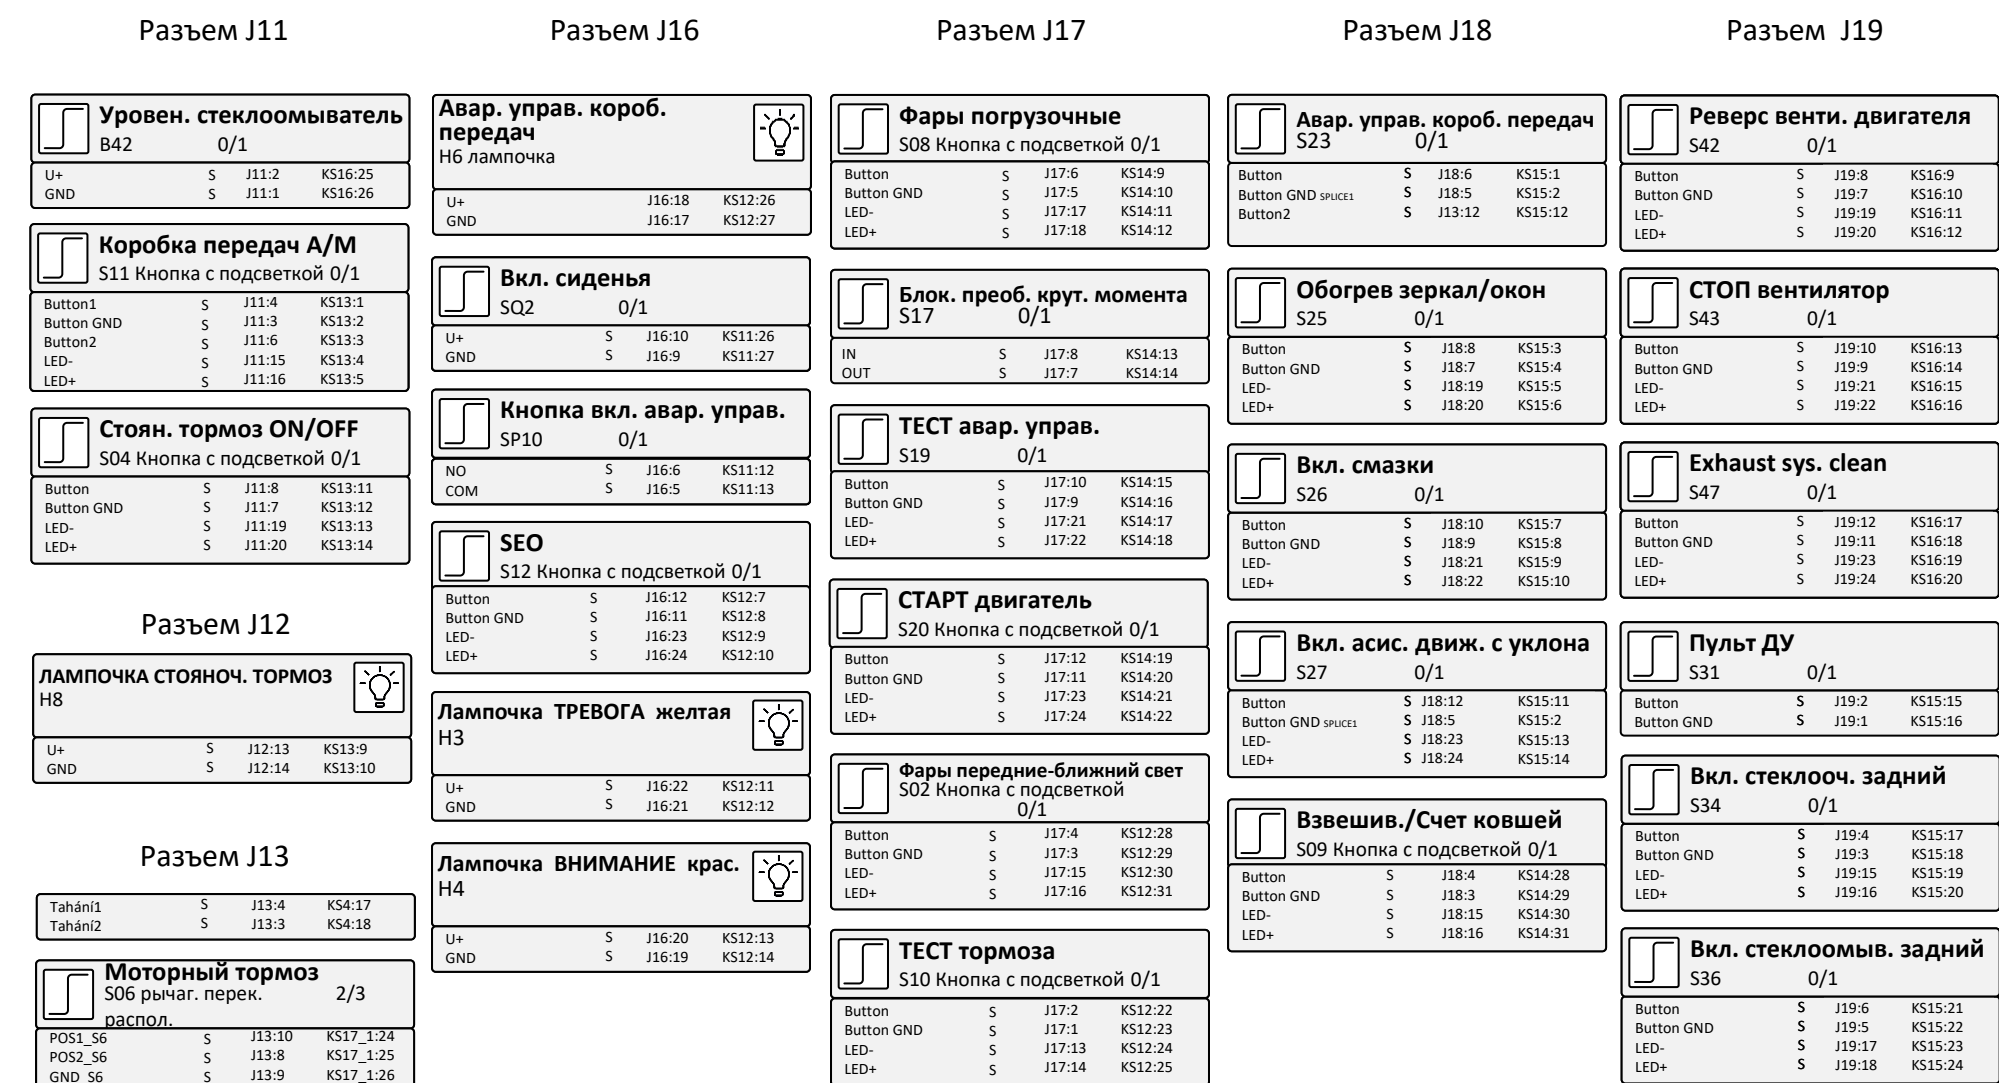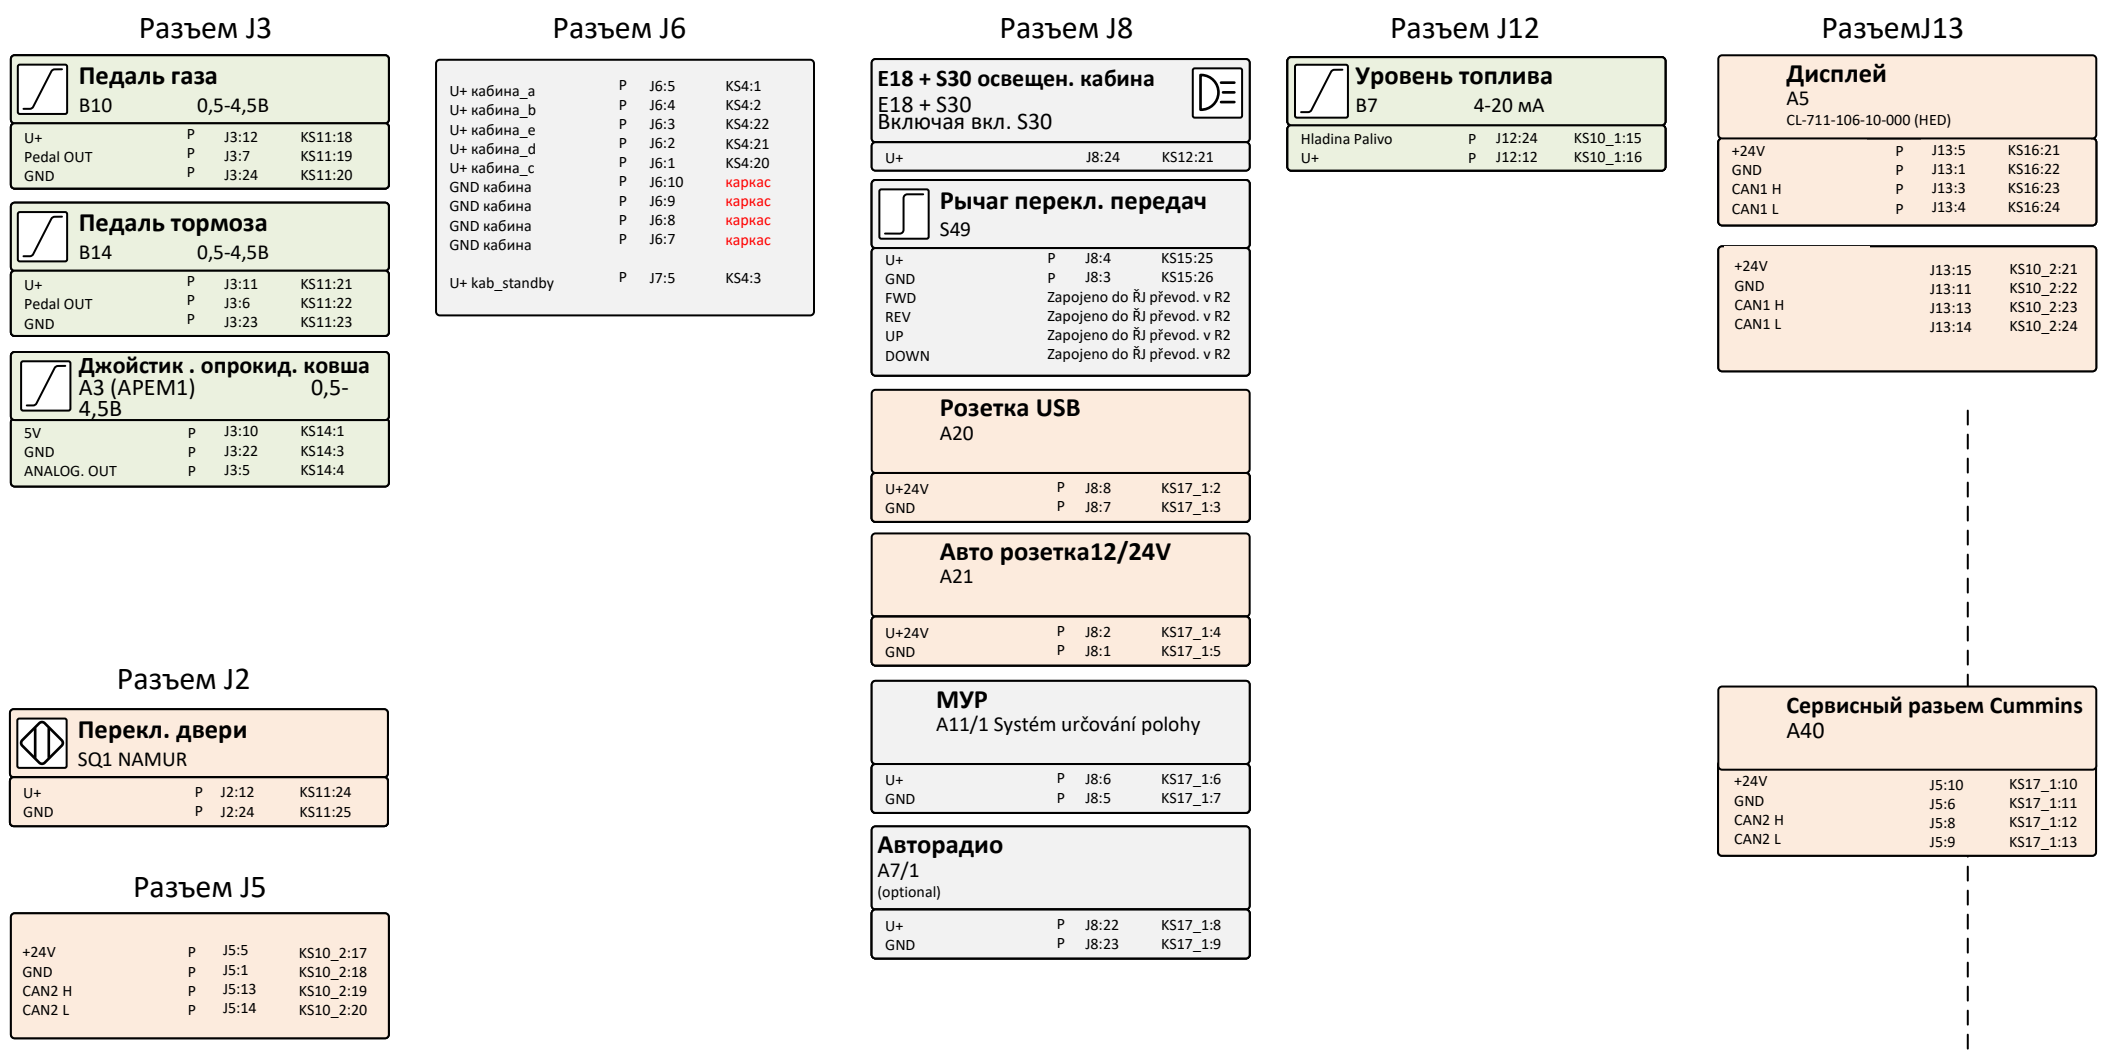

ПРИМЕЧАНИЕ: Ревизия изменений в индексах изменений находится на последней странице данного документа					
РАЗРАБОТАЛ: LAKOMÝ LUKÁŠ	ПРОВЕРИЛ: GREGOR PETR	ВИД ДОКУМЕНТА СТРУКТУРНАЯ СХЕМА	СТРАНИЦА: 6 OF 8	ДАТА: 9.1.2024	ФОРМАТ: A3
НАЗВАНИЕ: ШАХТНЫЙ САМОСВАЛ DSK30F			ДОПОЛНИТЕЛЬНОЕ НАЗВАНИЕ: РАСПРЕДЕЛИТЕЛЬ R5 MASTER		
	НОМЕР ЧЕРТЕЖА: 54Н-70-09000-9-01				ИНДЕКС ИЗМ.:

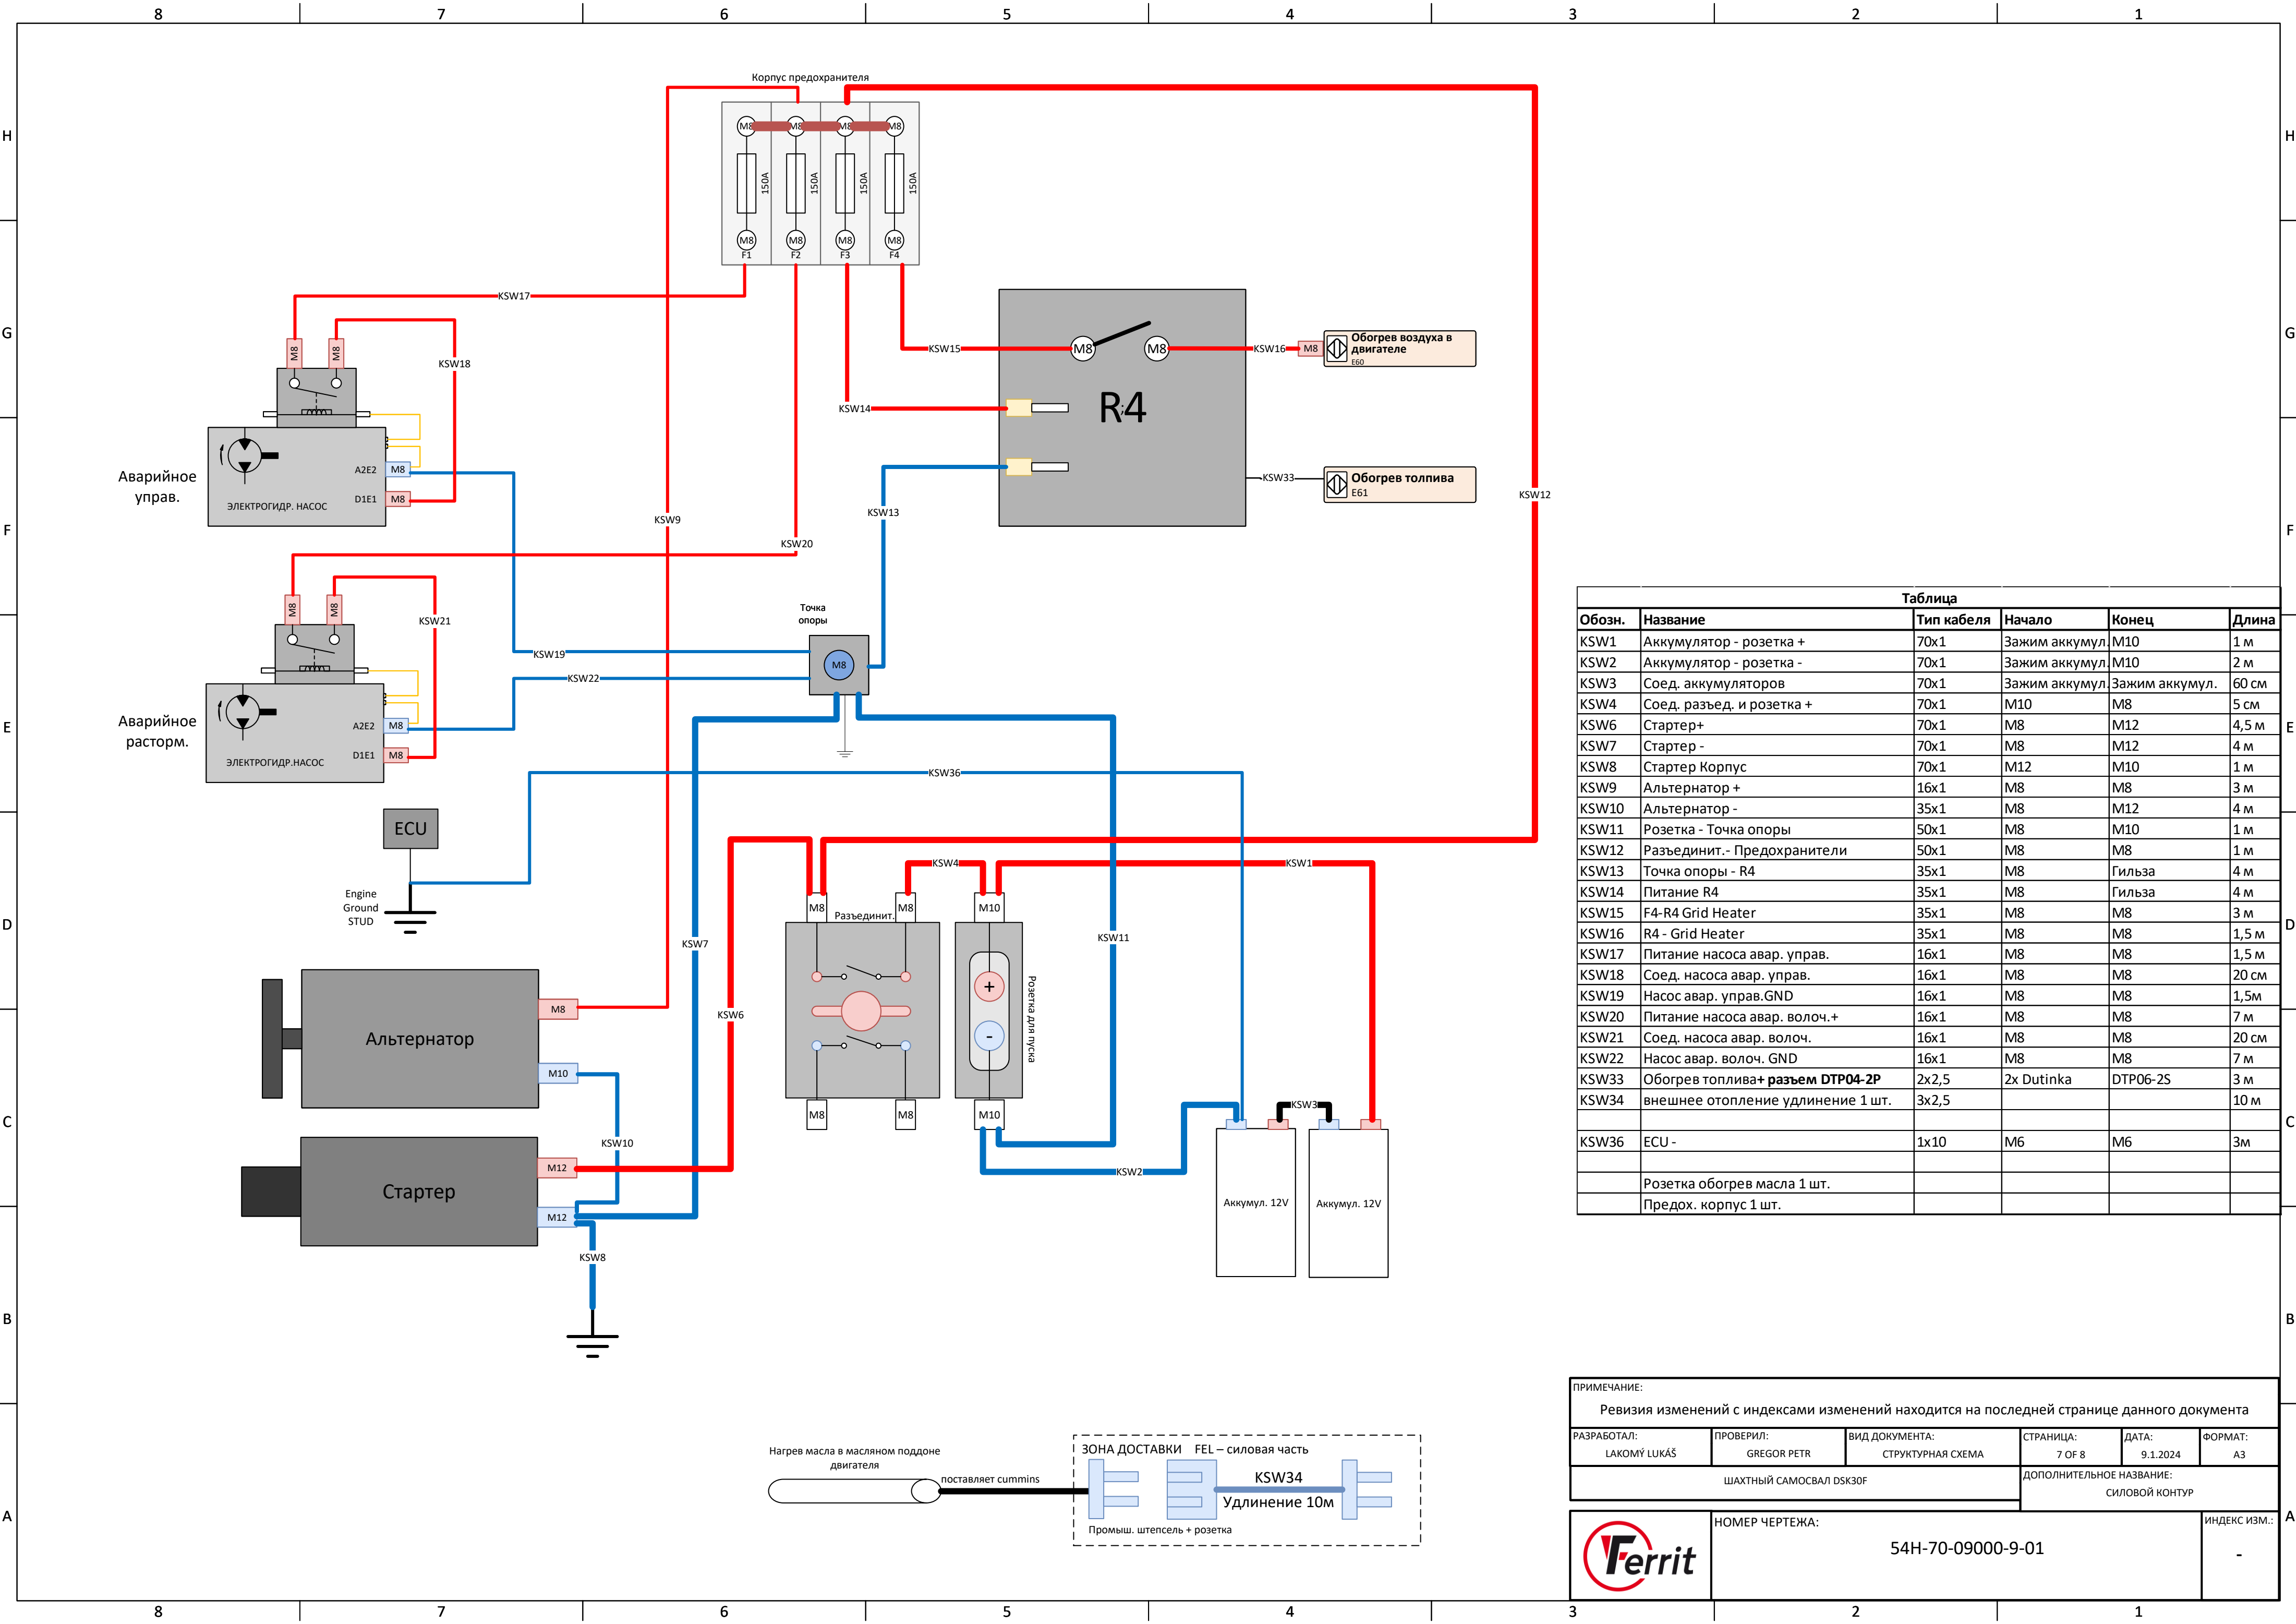


Таблица					
Обозн.	Название	Тип кабеля	Начало	Конец	Длина
KSW1	Аккумулятор - розетка +	70x1	Зажим аккумуля	M10	1 м
KSW2	Аккумулятор - розетка -	70x1	Зажим аккумуля	M10	2 м
KSW3	Соед. аккумуляторов	70x1	Зажим аккумуля	Зажим аккумуля.	60 см
KSW4	Соед. разъед. и розетка +	70x1	M10	M8	5 см
KSW6	Стартер+	70x1	M8	M12	4,5 м
KSW7	Стартер -	70x1	M8	M12	4 м
KSW8	Стартер Корпус	70x1	M12	M10	1 м
KSW9	Альтернатор +	16x1	M8	M8	3 м
KSW10	Альтернатор -	35x1	M8	M12	4 м
KSW11	Розетка - Точка опоры	50x1	M8	M10	1 м
KSW12	Разъединит.- Предохранители	50x1	M8	M8	1 м
KSW13	Точка опоры - R4	35x1	M8	Гильза	4 м
KSW14	Питание R4	35x1	M8	Гильза	4 м
KSW15	F4-R4 Grid Heater	35x1	M8	M8	3 м
KSW16	R4 - Grid Heater	35x1	M8	M8	1,5 м
KSW17	Питание насоса авар. управ.	16x1	M8	M8	1,5 м
KSW18	Соед. насоса авар. управ.	16x1	M8	M8	20 см
KSW19	Насос авар. управ.GND	16x1	M8	M8	1,5м
KSW20	Питание насоса авар. волоч.+	16x1	M8	M8	7 м
KSW21	Соед. насоса авар. волоч.	16x1	M8	M8	20 см
KSW22	Насос авар. волоч. GND	16x1	M8	M8	7 м
KSW33	Обогрев топлива+ разъем DTP04-2P	2x2,5	2x Dutinka	DTP06-2S	3 м
KSW34	внешнее отопление удлинение 1 шт.	3x2,5			10 м
KSW36	ECU -	1x10	M6	M6	3м
	Розетка обогрев масла 1 шт.				
	Предох. корпус 1 шт.				

ПРИМЕЧАНИЕ:
Ревизия изменений с индексами изменений находится на последней странице данного документа

РАЗРАБОТАЛ: LAKOMÝ LUKÁŠ	ПРОВЕРИЛ: GREGOR PETR	ВИД ДОКУМЕНТА: СТРУКТУРНАЯ СХЕМА	СТРАНИЦА: 7 OF 8	ДАТА: 9.1.2024	ФОРМАТ: A3
ШАХТНЫЙ САМОСВАЛ DSK30F			ДОПОЛНИТЕЛЬНОЕ НАЗВАНИЕ: СИЛОВОЙ КОНТУР		

НОМЕР ЧЕРТЕЖА:

54H-70-09000-9-01

ИНДЕКС ИЗМ.:

-

	8	7	6	5	4	3	2	1
H								
G								
F								
E								
D								
C								
B								
A								

ИНДЕКС ИЗМЕН.	ОПИСАНИЕ	ДАТА	АВТОР

ПРИМЕЧАНИЕ: Ревизия изменений с индексами изменений находится на последней странице данного документа					
РАЗРАБОТАЛ: LAKOMÝ LUKÁŠ	ПРОВЕРИЛ: GREGOR PETR	ВИД ДОКУМЕНТА: СТРУКТУРНАЯ СХЕМА	СТРАНИЦА: 8 OF 8	ДАТА: 9.1.2024	ФОРМАТ: A3
НАЗВАНИЕ: ШАХТНЫЙ САМОСВАЛ DSK30F			ДОПОЛНИТЕЛЬНОЕ НАЗВАНИЕ: РЕВИЗИЯ		
		НОМЕР ЧЕРТЕЖА: 54H-70-09000-9-01			ИНДЕКС ИЗМ.: -